
Received by Hobsons Bay City Council on 12/09/2025

Endorsed by Rhiannon Wright on 23/09/2025 under planning permit PA241413 on behalf of Hobsons Bay City Council. Sheet 1 of 7

BUILDING STRUCTURES
TO BE DEMOLISHED

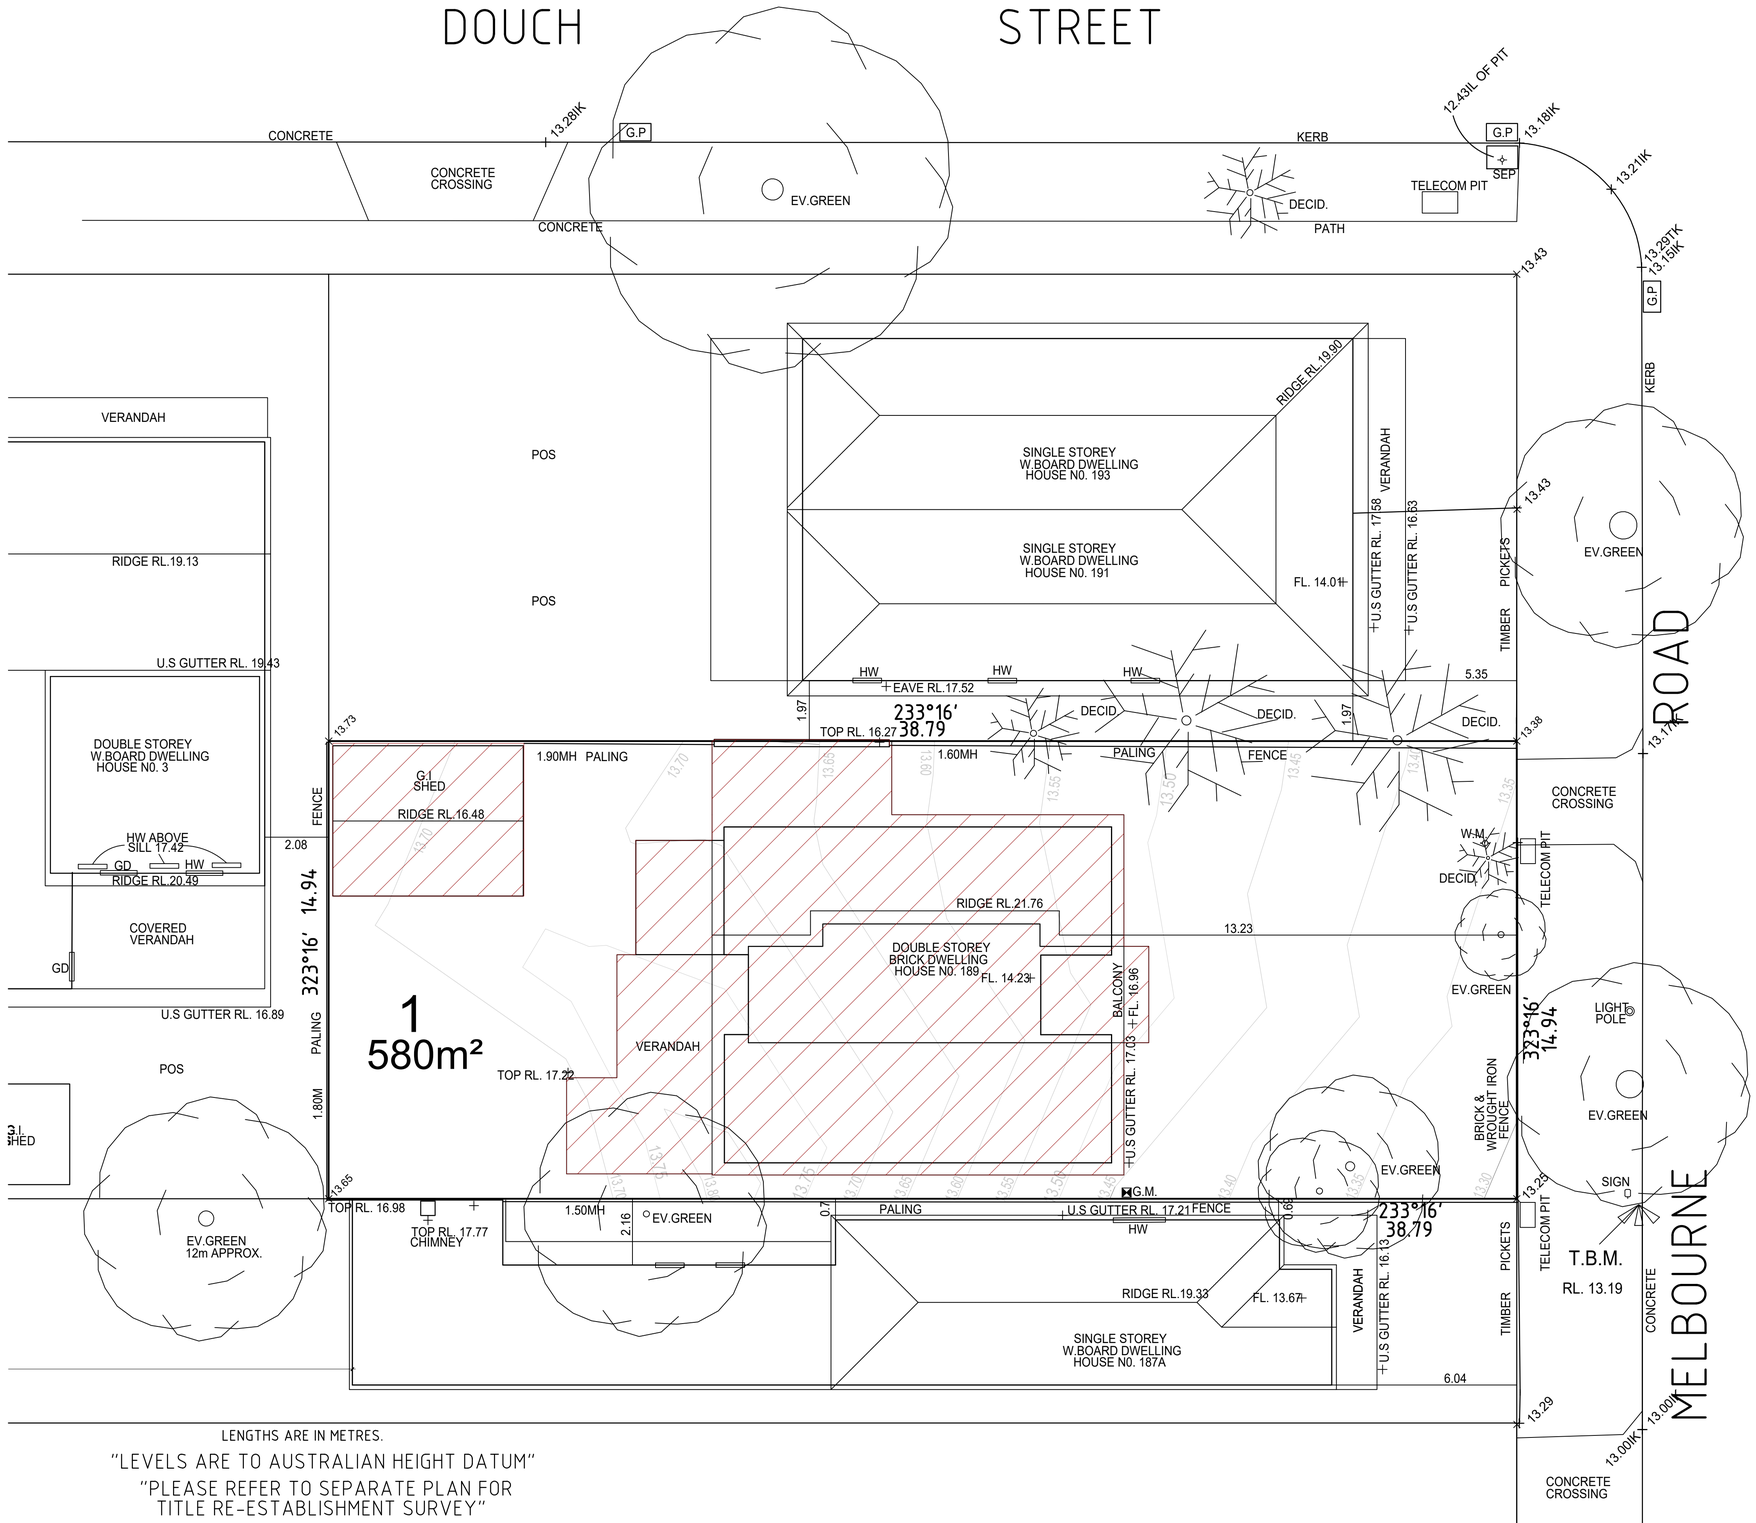

LENGTHS ARE IN METRES.

"LEVELS ARE TO AUSTRALIAN HEIGHT DATUM"

"PLEASE REFER TO SEPARATE PLAN FOR TITLE RE-ESTABLISHMENT SURVEY"

DEMOLITION PLAN

SCALE 1:100

THIS PAGE IS TO BE READ IN CONJUNCTION WITH COMPLETE ARCHITECTURAL PLANS AND ALL ENGINEERING AND SHOP DRAWINGS. WORK SHALL CONFORM TO THE SPECIFICATION, SPECIALISTS REPORTS, RELEVANT AUSTRALIAN REQUIREMENTS, AND LOCAL AUTHORITY REQUIREMENTS.
FIGURED DIMENSIONS TAKE PRECEDENCE OVER SCALED WORK.
BUILDER / CONTRACTOR TO VERIFY ALL DIMENSIONS & CHECK FOR DISCREPANCIES BETWEEN ARCHITECTURAL AND ALL OTHER DRAWINGS BEFORE ANY JOB COMMENCES.
THIS DRAWING IS PROTECTED BY COPY-RIGHT.
(CAD) A1

REV.	BY.	DATE.	DESCRIPTION.	REV.	BY.	DATE.	DESCRIPTION.
TP01	K.N.	02/08/24	TP SUBMISSION				
TP02	K.N.	08/10/24	RFI RESUBMISSION				
TP03	K.N.	19/11/24	RFI RESUBMISSION #1				
TP04	K.N.	01/04/25	RFI RESUBMISSION #2				
TP05	K.N.	07/04/25	RFI RESUBMISSION #3				

PROJECT.
TWO DOUBLE STOREY DEVELOPMENT
NO. 189 MELBOURNE ROAD
WILLIAMSTOWN ,VIC 3016

CLIENT.
--

JOB NO: MQ_24_034
DRAWN BY. MERAQ BUILDING DESIGNERS
SCALE: AS NOTATED
DATE. 02/08/2024

MERAQ
building designers
MERAQ PROJECTS
29 CABOT DRIVE, ALTONA NORTH 3025
P. 03 9391 0023 ABN. 85146959775
E. admin@meraq.com.au
Dajvis Andonov DP-AD37977
Onur Ozduzenciler DP-AD33253

#
DP

Received by Hobsons Bay City Council on 12/09/2025

Endorsed with changes made to plan on 23/09/2025 under planning permit PA241413 on behalf of Hobsons Bay City Council. Sheet 2 of 7

LEGEND

- COLOURED CONCRETE - AS PER COLOUR SCHEDULE SOLAR ABSORBENCY ≤0.7
- LAWN AND LANDSCAPED AREAS
- GARDEN BED - BLACK OR RED MULCH
- GROUND FLOOR ROOF UNDER (FIRST FLOOR PLAN ONLY)
- STORAGE — 6M3 STORAGE AREA PER DWELLING - HEIGHT TO BE LESS THAN ANY ADJACENT FENCING - GARAGE OVER-CAR STORAGE TO BE SHOWN IN ADDITIONAL DIAGRAM
- CLOTHESLINE RETRACTED BELOW 1.8M — FREE-STANDING CLOTHESLINE - NOT TO BE MOUNTED ON FENCES OR BOUNDARY WALLS - HEIGHT TO BE MAX. 1.8M
- 2000L WATER TANK — WATER TANK/S -OR- SOLAR HOT WATER — EACH DWELLING TO HAVE EITHER A WATER TANK OR A SOLAR HOT WATER SYSTEM.
- SOLAR HOT WATER SYSTEM (GAS BOOSTED)
- 2000L WATER TANK UNDER DECK
- BINS AS PER INDIVIDUAL COUNCIL REQUIREMENTS - WHERE LOCATED WITHIN GARAGES, EXHAUST FAN TO BE PROVIDED - WHERE LOCATED IN FRONT OF DWELLINGS, SCREENING AS NOTATED
- LETTER BOXES AS PER ELEVATIONS - NUMBERED AS PER DWELLING
- INDIVIDUAL CONCRETE PAVERS - SPACED TO ALLOW MIN. 20% PERMEABILITY
- METER BOXES AND METERS
- HWS — HOT WATER SYSTEM OR BOOSTER (WHERE EXTERNAL)
- H/AC — HEATING & COOLING SPLIT SYSTEM EXTERNAL CONDENSER
- SMOKE DETECTERS AS PER AS3786
- EXHAUST FANS VENTED EXTERNALLY AS PER AS1668.2
- 11.20/5.54 — NATURAL GROUND LEVELS TO A.H.D. UNLESS SPECIFIED OTHERWISE. FFL DENOTES FINISHED FLOOR LEVEL.
- EXISTING FENCE/S

DEVELOPMENT SUMMARY

DWELLING ONE (1)

DWELLING SIZE:		209.19 SQM
GROUND FLOOR:		122.20 SQM
FIRST FLOOR:		86.99 SQM
BEDROOMS:	4	
BATHROOMS:	3	
OFF STREET PARKING:	2	
FRONT SETBACK:		60.68 SQM
PRIVATE OPEN SPACE:		25.02 SQM
COURTYARD:		12.39 SQM
SITE COVERAGE:		136.32 SQM 23.50%

DWELLING TWO (2)

DWELLING SIZE:		214.89 SQM
GROUND FLOOR:		126.76 SQM
FIRST FLOOR:		88.13 SQM
BEDROOMS:	4	
BATHROOMS:	3	
OFF STREET PARKING:	2	
PRIVATE OPEN SPACE:		40.08 SQM
COURTYARD:		20.13 SQM
SITE COVERAGE:		126.07 SQM 22.60%

TOTAL

ALLOTMENT SIZE:	580.00 SQM
TOTAL GROUND AREA:	262.39 SQM
OFF STREET PARKING:	4 SPACES
PERMEABLE AREA:	189.26 SQM (32.26%)
SITE COVERAGE:	45.24%
GARDEN SPACE:	30.01%

TOWN PLANNING DRAWINGS ARE TO BE READ AS A WHOLE. NOTES ONLY INCLUDED ON AN INDIVIDUAL PAGE ARE STILL REQUIRED BY THE WHOLE PROPOSAL.

ELECTRICITY COMPANY CONNECTIONS TO THE PROPOSED DWELLING/S ARE TO BE PROVIDED UNDERGROUND.

ARBORIST REPORT - ALL WORKS TO BE CARRIED OUT IN ACCORDANCE WITH ARBORIST REPORT DATED 24TH OCTOBER 20204 PREPARED BY STEM ARBORICULTURE.

ALL STORM WATER INFRASTRUCTURE AS REQUIRED BY CONDITIONS OF THE PLANNING PERMIT ARE TO BE LOCATED WITHIN THE DRIVEWAY AND NOT IN THE AREAS SET ASIDE FOR LANDSCAPING.

ALFRESCO/DECK - ANY EXTERNAL LIVING AREAS (ALFRESCO, DECK, ETC) FOR EACH DWELLING IS NOT TO BE FULLY ENCLOSED AT ANY TIME. SIDE AND/OR REAR SECTION MUST BE LEFT OPEN TO PRIVATE OPEN SPACE.

PLANT AND EQUIPMENT - ALL EXTERNAL PLANT AND EQUIPMENT TO BE POSITIONED TO PREVENT UNREASONABLE NOISE AND VISUAL IMPACT.
POSITIONS OF ROOF FIXTURES (SUCH AS SKYLIGHTS, SOLARPANELS, CONDENSERS, ETC) ARE APPROXIMATE. LOCATIONS TBC WITH BUILDER & TRUSS MFR.

SERVICE PIPES, FITTINGS, & FIXTURES EXCLUDING DOWNPIPES TO BE CONCEALED ON EXPOSED ELEVATIONS TO THE SATISFACTION OF THE RESPONSIBLE AUTHORITY. DOWNPIPES TO BE PAINTED TO MATCH WALL FINISHES WHERE NECESSARY - REFER COLOUR SCHEDULE.

VISIBILITY SPLAYS AS PER CLAUSE 52.06-9, HAVE A CORNER SPLAY OR AREA AT LEAST 50 PER CENT CLEAR OF VISUAL OBSTRUCTIONS EXTENDING AT LEAST 2 METRES ALONG THE FRONTAGE ROAD FROM THE EDGE OF AN EXIT LANE AND 2.5 METRES ALONG THE EXIT LANE FROM THE FRONTAGE, TO PROVIDE A CLEAR VIEW OF PEDESTRIANS ON THE FOOTPATH OF THE FRONTAGE ROAD. THE AREA CLEAR OF VISUAL OBSTRUCTIONS MAY INCLUDE AN ADJACENT ENTRY OR EXIT LANE WHERE MORE THAN ONE LANE IS PROVIDED, OR ADJACENT LANDSCAPED AREAS, PROVIDED THE LANDSCAPING IN THOSE AREAS IS LESS THAN 900MM IN HEIGHT.

SUSTAINABILITY DESIGN ASSESSMENT WHERE ANY ADDITIONAL INFORMATION IS SUPPLIED WITHIN SDA, WSUD PLANS, STORM/MUSIC REPORTS, AND BESS REPORTS, ALL CONSTRUCTION MUST ALSO COMPLY WITH SPECIFICATIONS WITHIN THESE DOCUMENTS.

VEHICLE PARKING AREAS SET ASIDE FOR PARKED VEHICLES AND ACCESS LANES AS SHOWN ON THE ENDORSED PLANS MUST TO THE SATISFACTION OF THE RESPONSIBLE AUTHORITY BE:
a) CONSTRUCTED,
b) PROPERLY FORMED TO SUCH LEVELS THAT THEY CAN BE USED IN ACCORDANCE WITH THE PLANS,
c) SURFACED WITH ASPHALT OR CONCRETE UNLESS ANOTHER SURFACE TREATMENT IS APPROVED BY THE RESPONSIBLE AUTHORITY,
d) DRAINED AND MAINTAINED,
e) LINE-MARKED TO INDICATE EACH CAR SPACE AND ALL ACCESS LANES AND BE KEPT AVAILABLE FOR THESE PURPOSES AT ALL TIMES.
GARAGES MUST AT ALL TIMES BE KEPT AVAILABLE FOR PRIMARY PURPOSE OF PARKING MOTOR VEHICLES AND MUST NOT BE USED FOR ANY OTHER PURPOSE.


VEHICLE CROSSOVER
ANY VEHICLE CROSSINGS MUST BE CONSTRUCTED IN THE LOCATION SHOWN ON THE ENDORSED PLAN TO A STANDARD SATISFACTORY TO THE RESPONSIBLE AUTHORITY. THE RELOCATION OF ANY SERVICES INCLUDING ELECTRICITY POLES, DRAINAGE PITS, TELSTRA PITS, FIRE HYDRANTS AND THE LIKE MUST BE AT THE EXPENSE OF THE OWNER AND APPROVED BY THE APPROPRIATE AUTHORITY PRIOR TO UNDERTAKING SUCH WORKS. CONSENT FOR SUCH CROSSINGS MUST BE OBTAINED THROUGH COUNCIL'S CONTRACTS, PROCUREMENT AND ASSET PROTECTION DEPARTMENT PRIOR TO CONSTRUCTION.

TREE PROTECTION ZONES

A SUITABLE TREE PROTECTION ZONE OF 1.0M RADIUS WITH BARRIER FENCE MUST BE ESTABLISHED AROUND THE EXISTING STREET TREE ON THE SUBJECT SITE. THIS FENCE MUST NOT ENCLOSE THE FOOTPATH WHICH MUST BE KEPT CLEAR FOR PEDESTRIAN ACCESS AND A SIGN MUST BE ERECTED ON THE FENCE INFORMING THAT THE FENCE IS A 'TREE PROTECTION ZONE'.

TREE PROTECTION ZONE/S MUST BE ENCLOSED USING A 2 METER HIGH TEMPORARY CYCLONE FENCE OR SIMILAR, WHICH MUST REMAIN IN PLACE THROUGH ALL STAGES OF THE DEVELOPMENT. THIS FENCE MUST NOT ENCLOSE THE FOOTPATH WHICH MUST BE KEPT CLEAR FOR PEDESTRIAN ACCESS AND A SIN,S MUST BE ERECTED ON THE FENCE INFORMING THAT THE FENCE IS A 'TREE PROTECTION ZONE'. THE AREA WITHIN THE TREE PROTECTION ZONE MUST NOT BE DISTURBED BY ANY MEANS (INCL. PARKING OF VEHICLES OR STORAGE OF PLANT & EQUIPMENT, MATERIALS, SOIL OR WASTE). NO EXCAVATION IS ALLOWED WITHIN THE TREE PROTECTION ZONE EXCEPT WITH THE CONSENT OF COUNCIL'S TOWN PLANNING DEPARTMENT & UNDER THE SUPERVISION OF A QUALIFIED ARBORIST.

- ADVANCED CANOPY TREES 1.5M TALL AT TIME OF PLANTING
- TREE PROTECTION ZONE BARRIER FENCE
- EXISTING TREES TO BE REMOVED
- EXISTING TREES TO REMAIN

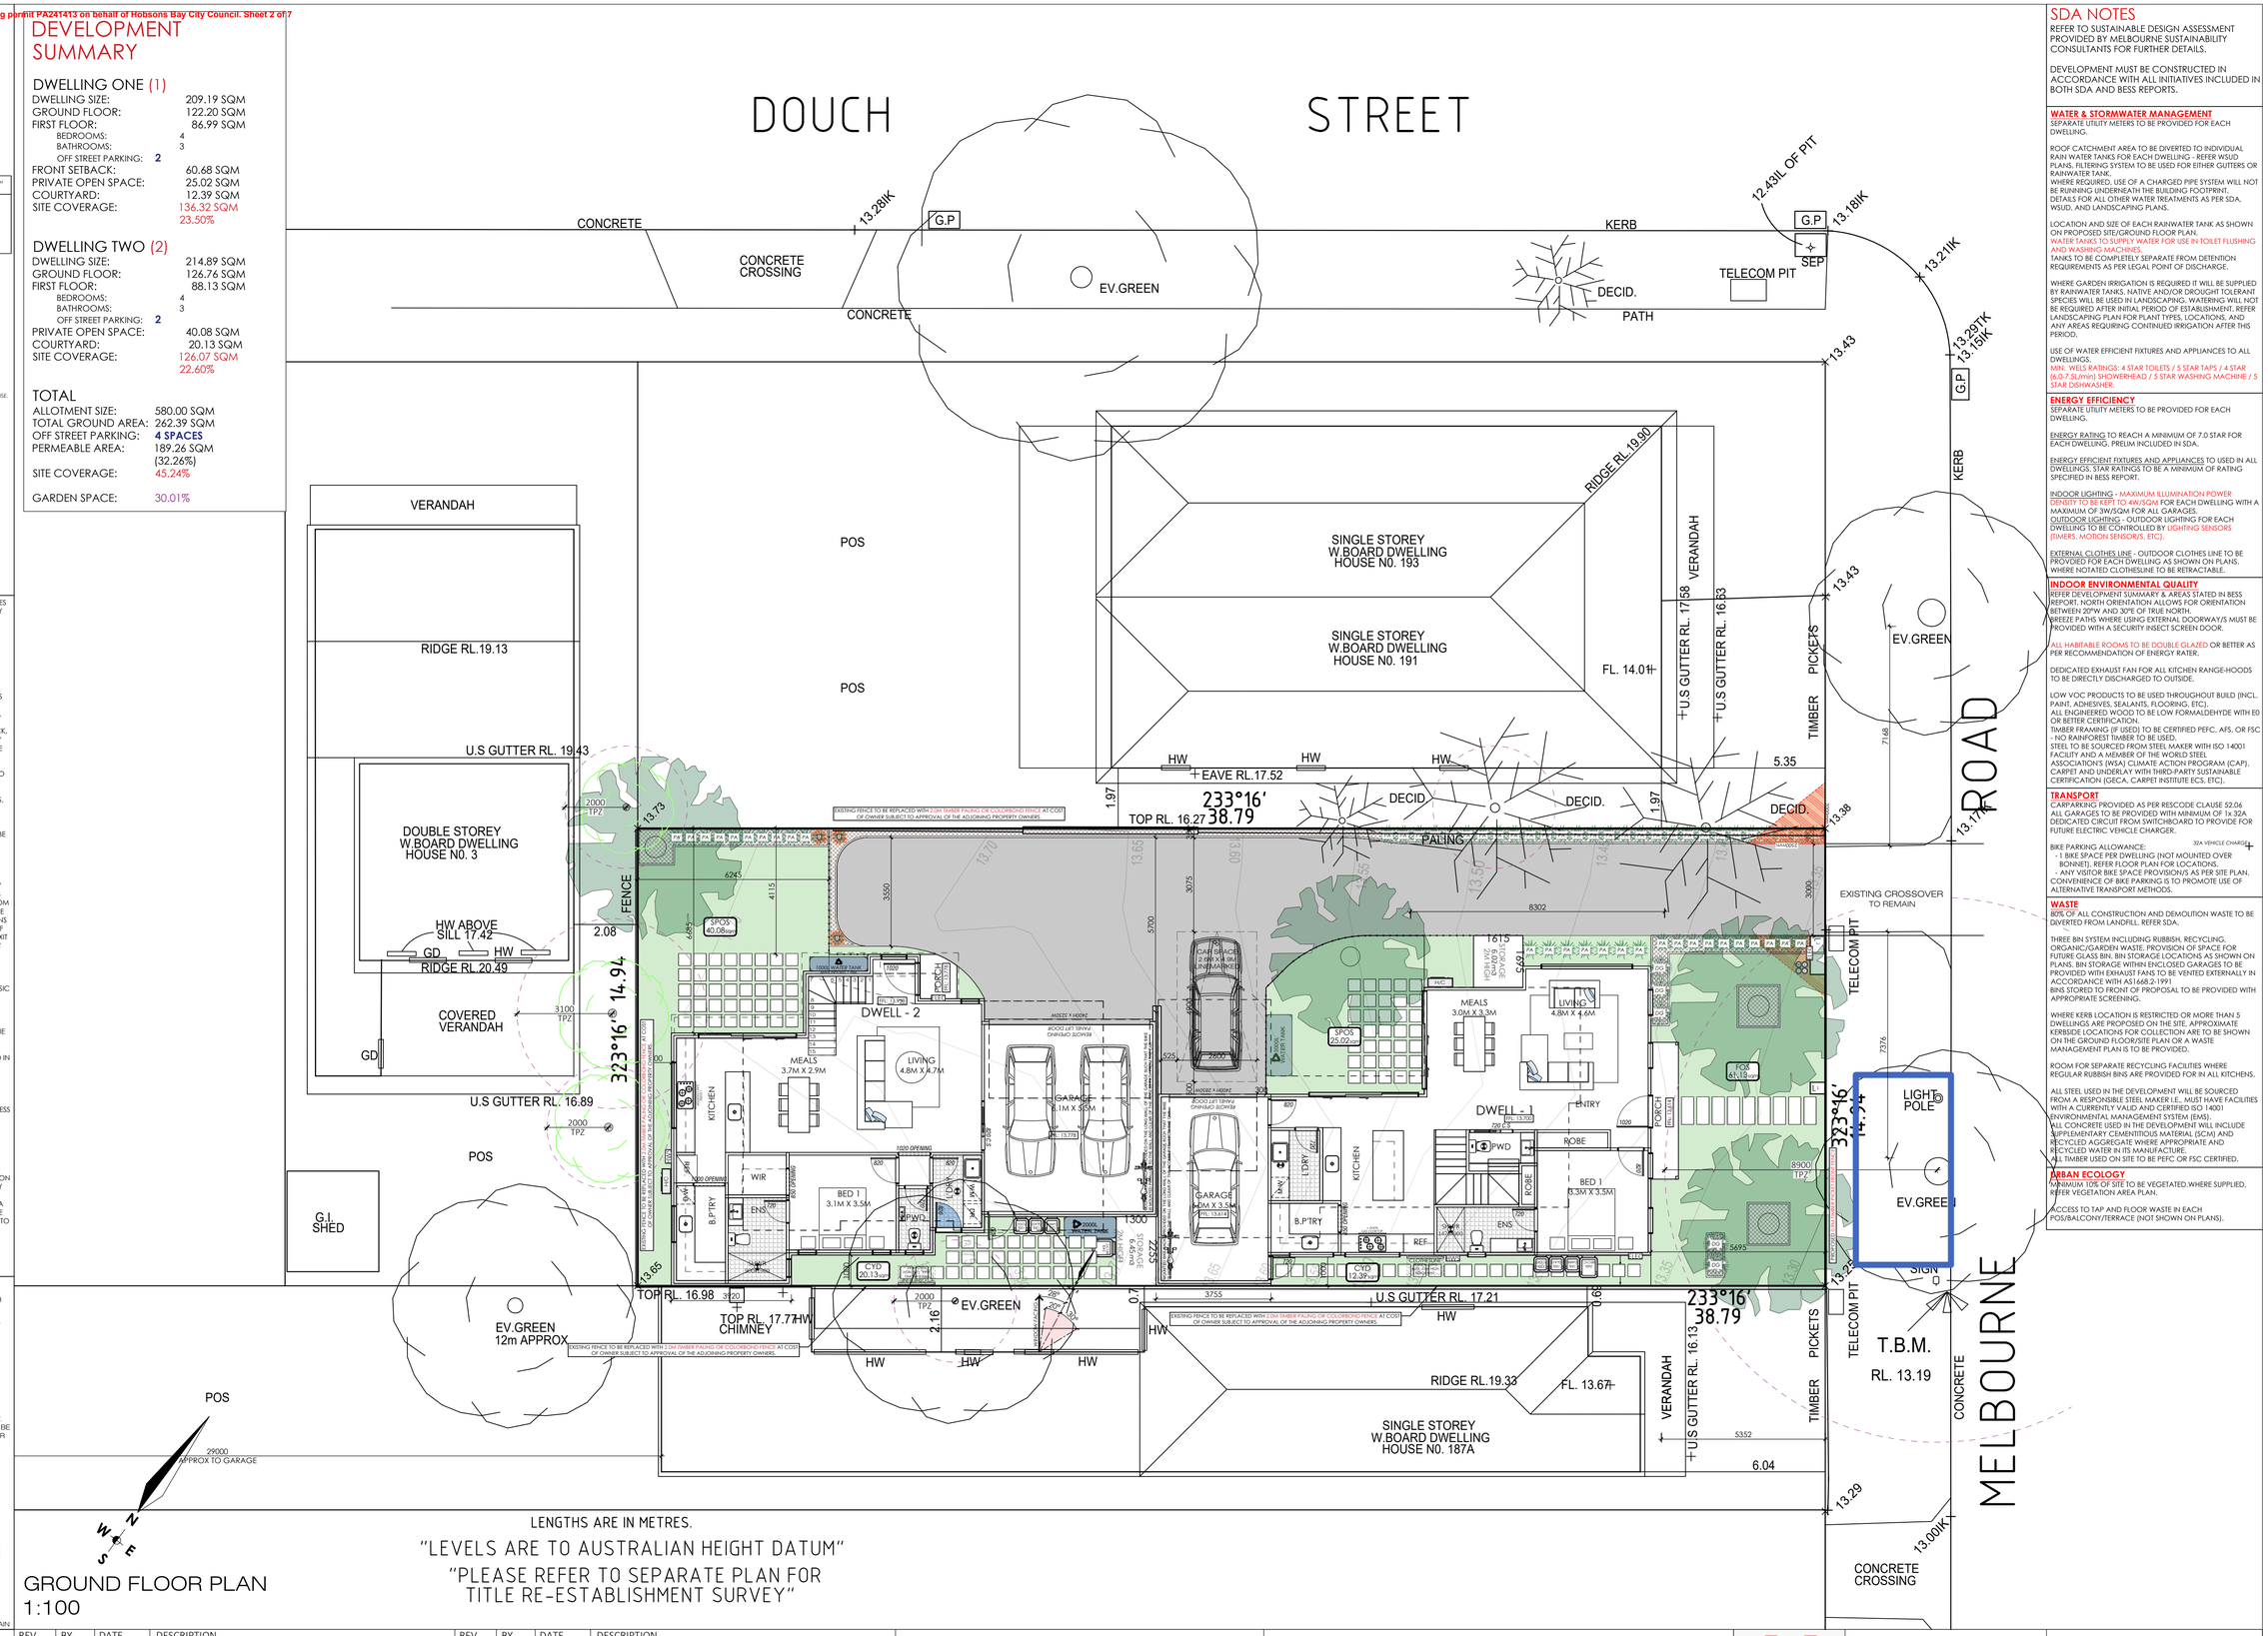

POS
29000
APPROX TO GARAGE

GROUND FLOOR PLAN
1:100

SDA NOTES

REFER TO SUSTAINABLE DESIGN ASSESSMENT PROVIDED BY MELBOURNE SUSTAINABILITY CONSULTANTS FOR FURTHER DETAILS.

DEVELOPMENT MUST BE CONSTRUCTED IN ACCORDANCE WITH ALL INITIATIVES INCLUDED IN BOTH SDA AND BESS REPORTS.

WATER & STORMWATER MANAGEMENT
SEPARATE UTILITY METERS TO BE PROVIDED FOR EACH DWELLING.

ROOF CATCHMENT AREA TO BE DIVERTED TO INDIVIDUAL RAIN WATER TANKS FOR EACH DWELLING - REFER WSUD PLANS. FILTERING SYSTEM TO BE USED FOR EITHER GUTTERS OR RAINWATER TANK.
WHERE REQUIRED, USE OF A CHARGED PIPE SYSTEM WILL NOT BE RUNNING UNDERNEATH THE BUILDING FOOTPRINT. DETAILS FOR ALL OTHER WATER TREATMENTS AS PER SDA, WSUD, AND LANDSCAPING PLANS.

LOCATION AND SIZE OF EACH RAINWATER TANK AS SHOWN ON PROPOSED SITE/GROUND FLOOR PLAN.
WATER TANKS TO SUPPLY WATER FOR USE IN TOILET FLUSHING AND WASHING MACHINES.
TANKS TO BE COMPLETELY SEPARATE FROM DETENTION REQUIREMENTS AS PER LEGAL POINT OF DISCHARGE.

WHERE GARDEN IRRIGATION IS REQUIRED IT WILL BE SUPPLIED BY RAINWATER TANKS. NATIVE AND/OR DROUGHT TOLERANT SPECIES WILL BE USED IN LANDSCAPING. WATERING WILL NOT BE REQUIRED AFTER INITIAL PERIOD OF ESTABLISHMENT. REFER LANDSCAPING PLAN FOR PLANT TYPES, LOCATIONS, AND ANY AREAS REQUIRING CONTINUED IRRIGATION AFTER THIS PERIOD.

USE OF WATER EFFICIENT FIXTURES AND APPLIANCES TO ALL DWELLINGS.
MIN. WELS RATINGS: 4 STAR TOILETS / 5 STAR TAPS / 4 STAR (6.0-7.5L/min) SHOWERHEAD / 5 STAR WASHING MACHINE / 5 STAR DISHWASHER.

ENERGY EFFICIENCY
SEPARATE UTILITY METERS TO BE PROVIDED FOR EACH DWELLING.

ENERGY RATING TO REACH A MINIMUM OF 7.0 STAR FOR EACH DWELLING. PRELIM INCLUDED IN SDA.

ENERGY EFFICIENT FIXTURES AND APPLIANCES TO USED IN ALL DWELLINGS. STAR RATINGS TO BE A MINIMUM OF RATING SPECIFIED IN BESS REPORT.

INDOOR LIGHTING - MAXIMUM ILLUMINATION POWER DENSITY TO BE KEPT TO 4W/SQM FOR EACH DWELLING WITH A MAXIMUM OF 3W/SQM FOR ALL GARAGES.
OUTDOOR LIGHTING - OUTDOOR LIGHTING FOR EACH DWELLING TO BE CONTROLLED BY LIGHTING SENSORS (TIMERS, MOTION SENSOR/S, ETC).

EXTERNAL CLOTHES LINE - OUTDOOR CLOTHES LINE TO BE PROVIDED FOR EACH DWELLING AS SHOWN ON PLANS, WHERE NOTATED CLOTHESLINE TO BE RETRACTABLE.

INDOOR ENVIRONMENTAL QUALITY
REFER DEVELOPMENT SUMMARY & AREAS STATED IN BESS REPORT. NORTH ORIENTATION ALLOWS FOR ORIENTATION BETWEEN 20°W AND 30°E OF TRUE NORTH.
BREEZE PATHS WHERE USING EXTERNAL DOORWAY/S MUST BE PROVIDED WITH A SECURITY INSECT SCREEN DOOR.

ALL HABITABLE ROOMS TO BE DOUBLE GLAZED OR BETTER AS PER RECOMMENDATION OF ENERGY RATER.

DEDICATED EXHAUST FAN FOR ALL KITCHEN RANGE-HOODS TO BE DIRECTLY DISCHARGED TO OUTSIDE.

LOW VOC PRODUCTS TO BE USED THROUGHOUT BUILD (INCL. PAINT, ADHESIVES, SEALANTS, FLOORING, ETC),
ALL ENGINEERED WOOD TO BE LOW FORMALDEHYDE WITH E0 OR BETTER CERTIFICATION.
TIMBER FRAMING (IF USED) TO BE CERTIFIED FEFC, AFS, OR FSC
- NO RAINFOREST TIMBER TO BE USED.
STEEL TO BE SOURCED FROM STEEL MAKER WITH ISO 14001 FACILITY AND A MEMBER OF THE WORLD STEEL ASSOCIATION'S (WSA) CLIMATE ACTION PROGRAM (CAP).
CARPET AND UNDERLAY WITH THIRD-PARTY SUSTAINABLE CERTIFICATION (GECA, CARPET INSTITUTE ECS, ETC).

TRANSPORT
CARPARKING PROVIDED AS PER RESCODE CLAUSE 52.06
ALL GARAGES TO BE PROVIDED WITH MINIMUM OF 1x 32A DEDICATED CIRCUIT FROM SWITCHBOARD TO PROVIDE FOR FUTURE ELECTRIC VEHICLE CHARGER.

BIKE PARKING ALLOWANCE: 32A VEHICLE CHARGER
- 1 BIKE SPACE PER DWELLING (NOT MOUNTED OVER BONNET). REFER FLOOR PLAN FOR LOCATIONS.
- ANY VISITOR BIKE SPACE PROVISION/S AS PER SITE PLAN. CONVENIENCE OF BIKE PARKING IS TO PROMOTE USE OF ALTERNATIVE TRANSPORT METHODS.

WASTE
80% OF ALL CONSTRUCTION AND DEMOLITION WASTE TO BE DIVERTED FROM LANDFILL. REFER SDA.

THREE BIN SYSTEM INCLUDING RUBBISH, RECYCLING, ORGANIC/GARDEN WASTE. PROVISION OF SPACE FOR FUTURE GLASS BIN. BIN STORAGE LOCATIONS AS SHOWN ON PLANS. BIN STORAGE WITHIN ENCLOSED GARAGES TO BE PROVIDED WITH EXHAUST FANS TO BE VENTED EXTERNALLY IN ACCORDANCE WITH AS1668.2-1991
BINS STORED TO FRONT OF PROPOSAL TO BE PROVIDED WITH APPROPRIATE SCREENING.

WHERE KERB LOCATION IS RESTRICTED OR MORE THAN 5 DWELLINGS ARE PROPOSED ON THE SITE, APPROXIMATE KERBSIDE LOCATIONS FOR COLLECTION ARE TO BE SHOWN ON THE GROUND FLOOR/SITE PLAN OR A WASTE MANAGEMENT PLAN IS TO BE PROVIDED.

ROOM FOR SEPARATE RECYCLING FACILITIES WHERE REGULAR RUBBISH BINS ARE PROVIDED FOR IN ALL KITCHENS.

ALL STEEL USED IN THE DEVELOPMENT WILL BE SOURCED FROM A RESPONSIBLE STEEL MAKER I.E., MUST HAVE FACILITIES WITH A CURRENTLY VALID AND CERTIFIED ISO 14001 ENVIRONMENTAL MANAGEMENT SYSTEM (EMS).
ALL CONCRETE USED IN THE DEVELOPMENT WILL INCLUDE SUPPLEMENTARY CEMENTITIOUS MATERIAL (SCM) AND RECYCLED AGGREGATE WHERE APPROPRIATE AND RECYCLED WATER IN ITS MANUFACTURE.
ALL TIMBER USED ON SITE TO BE PEFC OR FSC CERTIFIED.

URBAN ECOLOGY
A MINIMUM 10% OF SITE TO BE VEGETATED.WHERE SUPPLIED, REFER VEGETATION AREA PLAN.

ACCESS TO TAP AND FLOOR WASTE IN EACH POS/BALCONY/TERRACE (NOT SHOWN ON PLANS).

THIS PAGE IS TO BE READ IN CONJUNCTION WITH COMPLETE ARCHITECTURAL PLANS AND ALL ENGINEERING AND SHOP DRAWINGS. WORK SHALL CONFORM TO THE SPECIFICATION, SPECIALISTS REPORTS, RELEVANT AUSTRALIAN REQUIREMENTS, AND LOCAL AUTHORITY REQUIREMENTS.
FIGURED DIMENSIONS TAKE PRECEDENCE OVER SCALED WORK. BUILDER / CONTRACTOR TO VERIFY ALL DIMENSIONS & CHECK FOR DISCREPANCIES BETWEEN ARCHITECTURAL AND ALL OTHER DRAWINGS BEFORE ANY JOB COMMENCES.
THIS DRAWING IS PROTECTED BY COPY-RIGHT.
(CAD) A1

REV.	BY.	DATE.	DESCRIPTION.	REV.	BY.	DATE.	DESCRIPTION.
TP01	K.N.	02/08/24	TP SUBMISSION				
TP02	K.N.	08/10/24	RFI RESUBMISSION				
TP03	K.N.	19/11/24	RFI RESUBMISSION #1				
TP04	K.N.	01/04/25	RFI RESUBMISSION #2				

PROJECT.
TWO DOUBLE STOREY DEVELOPMENT
NO. 189 MELBOURNE ROAD
WILLIAMSTOWN ,VIC 3016

CLIENT.
--

JOB NO: MQ_24_034
DRAWN BY. MERAQ BUILDING DESIGNERS
SCALE: AS NOTATED
DATE. 11/06/2025

MERAQ PROJECTS
29 CABOT DRIVE, ALTONA NORTH 3025
P. 03 9391 0023 ABN. 85146959775
E. admin@meraq.com.au
Dajvis Andonov DP-AD37977
Onur Ozduzenciler DP-AD33253

#
01

Received by Hobsons Bay City Council on 12/09/2025

Endorsed with changes made right on 23/09/2025 under planning permit PA241413 on behalf of Hobsons Bay City Council. Sheet 3 of 7

LEGEND

- COLOURED CONCRETE - AS PER COLOUR SCHEDULE SOLAR ABSORBENCY ≤0.7
- LAWN AND LANDSCAPED AREAS
- GARDEN BED - BLACK OR RED MULCH
- GROUND FLOOR ROOF UNDER (FIRST FLOOR PLAN ONLY)
- STORAGE — 6M3 STORAGE AREA PER DWELLING - HEIGHT TO BE LESS THAN ANY ADJACENT FENCING - GARAGE OVER-CAR STORAGE TO BE SHOWN IN ADDITIONAL DIAGRAM
- CLOTHESLINE (MOUNTED BELOW 1.8M) — FREE-STANDING CLOTHESLINE - NOT TO BE MOUNTED ON FENCES OR BOUNDARY WALLS - HEIGHT TO BE MAX. 1.8M
- 2000L WATER TANK — WATER TANK/S -OR- SOLAR HOT WATER — EACH DWELLING TO HAVE EITHER A WATER TANK OR A SOLAR HOT WATER SYSTEM. (SOLAR HOT WATER SYSTEM (GAS BOOSTED))
- 2000L WATER TANK (UNDER DECK)
- BINS AS PER INDIVIDUAL COUNCIL REQUIREMENTS - WHERE LOCATED WITHIN GARAGES, EXHAUST FAN TO BE PROVIDED - WHERE LOCATED IN FRONT OF DWELLINGS, SCREENING AS NOTATED
- LETTER BOXES AS PER ELEVATIONS - NUMBERED AS PER DWELLING
- INDIVIDUAL CONCRETE PAVERS - SPACED TO ALLOW MIN. 20% PERMEABILITY
- METER BOXES AND METERS
- HWS — HOT WATER SYSTEM OR BOOSTER (WHERE EXTERNAL)
- H/AC — HEATING & COOLING SPLIT SYSTEM EXTERNAL CONDENSER
- SMOKE DETECTERS AS PER AS3786
- EXHAUST FANS VENTED EXTERNALLY AS PER AS1668.2
- +RL.xx.xx — NATURAL GROUND LEVELS TO A H.D. UNLESS SPECIFIED OTHERWISE. FFL DENOTES FINISHED FLOOR LEVEL.
- EXISTING FENCE/S

DEVELOPMENT SUMMARY

DWELLING ONE (1)

DWELLING SIZE:		209.19 SQM
GROUND FLOOR:		122.20 SQM
FIRST FLOOR:		86.99 SQM
BEDROOMS:	4	
BATHROOMS:	3	
OFF STREET PARKING:	2	
FRONT SETBACK:		60.68 SQM
PRIVATE OPEN SPACE:		25.02 SQM
COURTYARD:		12.39 SQM
SITE COVERAGE:		136.32 SQM 23.50%

DWELLING TWO (2)

DWELLING SIZE:		214.89 SQM
GROUND FLOOR:		126.76 SQM
FIRST FLOOR:		88.13 SQM
BEDROOMS:	4	
BATHROOMS:	3	
OFF STREET PARKING:	2	
PRIVATE OPEN SPACE:		40.08 SQM
COURTYARD:		20.13 SQM
SITE COVERAGE:		126.07 SQM 22.60%

TOTAL

ALLOTMENT SIZE:	580.00 SQM
TOTAL GROUND AREA:	262.39 SQM
OFF STREET PARKING:	4 SPACES
PERMEABLE AREA:	189.26 SQM (32.26%)
SITE COVERAGE:	45.24%
GARDEN SPACE:	30.01%

TOWN PLANNING DRAWINGS ARE TO BE READ AS A WHOLE. NOTES ONLY INCLUDED ON AN INDIVIDUAL PAGE ARE STILL REQUIRED BY THE WHOLE PROPOSAL.

ELECTRICITY COMPANY CONNECTIONS TO THE PROPOSED DWELLING/S ARE TO BE PROVIDED UNDERGROUND.

ARBORIST REPORT - ALL WORKS TO BE CARRIED OUT IN ACCORDANCE WITH ARBORIST REPORT DATED 24TH OCTOBER 20204 PREPARED BY STEM ARBORICULTURE.

ALL STORM WATER INFRASTRUCTURE AS REQUIRED BY CONDITIONS OF THE PLANNING PERMIT ARE TO BE LOCATED WITHIN THE DRIVEWAY AND NOT IN THE AREAS SET ASIDE FOR LANDSCAPING.

ALFRESCO/DECK - ANY EXTERNAL LIVING AREAS (ALFRESCO, DECK, ETC) FOR EACH DWELLING IS NOT TO BE FULLY ENCLOSED AT ANY TIME. SIDE AND/OR REAR SECTION MUST BE LEFT OPEN TO PRIVATE OPEN SPACE.

PLANT AND EQUIPMENT - ALL EXTERNAL PLANT AND EQUIPMENT TO BE POSITIONED TO PREVENT UNREASONABLE NOISE AND VISUAL IMPACT.
POSITIONS OF ROOF FIXTURES (SUCH AS SKYLIGHTS, SOLARPANELS, CONDENSERS, ETC) ARE APPROXIMATE. LOCATIONS TBC WITH BUILDER & TRUSS MFR.

SERVICE PIPES, FITTINGS, & FIXTURES EXCLUDING DOWNPIPES TO BE CONCEALED ON EXPOSED ELEVATIONS TO THE SATISFACTION OF THE RESPONSIBLE AUTHORITY. DOWNPIPES TO BE PAINTED TO MATCH WALL FINISHES WHERE NECESSARY - REFER COLOUR SCHEDULE.

VISIBILITY SPLAYS AS PER CLAUSE 52.06-9, HAVE A CORNER SPLAY OR AREA AT LEAST 50 PER CENT CLEAR OF VISUAL OBSTRUCTIONS EXTENDING AT LEAST 2 METRES ALONG THE FRONTAGE ROAD FROM THE EDGE OF AN EXIT LANE AND 2.5 METRES ALONG THE EXIT LANE FROM THE FRONTAGE, TO PROVIDE A CLEAR VIEW OF PEDESTRIANS ON THE FOOTPATH OF THE FRONTAGE ROAD. THE AREA CLEAR OF VISUAL OBSTRUCTIONS MAY INCLUDE AN ADJACENT ENTRY OR EXIT LANE WHERE MORE THAN ONE LANE IS PROVIDED, OR ADJACENT LANDSCAPED AREAS, PROVIDED THE LANDSCAPING IN THOSE AREAS IS LESS THAN 900MM IN HEIGHT.

SUSTAINABILITY DESIGN ASSESSMENT WHERE ANY ADDITIONAL INFORMATION IS SUPPLIED WITHIN SDA, WSUD PLANS, STORM/MUSIC REPORTS, AND BESS REPORTS, ALL CONSTRUCTION MUST ALSO COMPLY WITH SPECIFICATIONS WITHIN THESE DOCUMENTS.

VEHICLE PARKING AREAS SET ASIDE FOR PARKED VEHICLES AND ACCESS LANES AS SHOWN ON THE ENDORSED PLANS MUST TO THE SATISFACTION OF THE RESPONSIBLE AUTHORITY BE:
a) CONSTRUCTED.
b) PROPERLY FORMED TO SUCH LEVELS THAT THEY CAN BE USED IN ACCORDANCE WITH THE PLANS.
c) SURFACED WITH ASPHALT OR CONCRETE UNLESS ANOTHER SURFACE TREATMENT IS APPROVED BY THE RESPONSIBLE AUTHORITY.
d) DRAINED AND MAINTAINED.
e) LINE-MARKED TO INDICATE EACH CAR SPACE AND ALL ACCESS LANES AND BE KEPT AVAILABLE FOR THESE PURPOSES AT ALL TIMES.
GARAGES MUST AT ALL TIMES BE KEPT AVAILABLE FOR PRIMARY PURPOSE OF PARKING MOTOR VEHICLES AND MUST NOT BE USED FOR ANY OTHER PURPOSE.


VEHICLE CROSSOVER
ANY VEHICLE CROSSINGS MUST BE CONSTRUCTED IN THE LOCATION SHOWN ON THE ENDORSED PLAN TO A STANDARD SATISFACTORY TO THE RESPONSIBLE AUTHORITY. THE RELOCATION OF ANY SERVICES INCLUDING ELECTRICITY POLES, DRAINAGE PITS, TELSTRA PITS, FIRE HYDRANTS AND THE LIKE MUST BE AT THE EXPENSE OF THE OWNER AND APPROVED BY THE APPROPRIATE AUTHORITY PRIOR TO UNDERTAKING SUCH WORKS. CONSENT FOR SUCH CROSSINGS MUST BE OBTAINED THROUGH COUNCIL'S CONTRACTS, PROCUREMENT AND ASSET PROTECTION DEPARTMENT PRIOR TO CONSTRUCTION.

TREE PROTECTION ZONES

A SUITABLE TREE PROTECTION ZONE OF 1.0M RADIUS WITH BARRIER FENCE MUST BE ESTABLISHED AROUND THE EXISTING STREET TREE ON THE SUBJECT SITE. THIS FENCE MUST NOT ENCLOSE THE FOOTPATH WHICH MUST BE KEPT CLEAR FOR PEDESTRIAN ACCESS AND A SIGN MUST BE ERECTED ON THE FENCE INFORMING THAT THE FENCE IS A 'TREE PROTECTION ZONE'.

TREE PROTECTION ZONE/S MUST BE ENCLOSED USING A 2 METER HIGH TEMPORARY CYCLONE FENCE OR SIMILAR, WHICH MUST REMAIN IN PLACE THROUGH ALL STAGES OF THE DEVELOPMENT. THIS FENCE MUST NOT ENCLOSE THE FOOTPATH WHICH MUST BE KEPT CLEAR FOR PEDESTRIAN ACCESS AND A SING MUST BE ERECTED ON THE FENCE INFORMING THAT THE FENCE IS A 'TREE PROTECTION ZONE'. THE AREA WITHIN THE TREE PROTECTION ZONE MUST NOT BE DISTURBED BY ANY MEANS (INCL. PARKING OF VEHICLES OR STORAGE OF PLANT & EQUIPMENT, MATERIALS, SOIL OR WASTE). NO EXCAVATION IS ALLOWED WITHIN THE TREE PROTECTION ZONE EXCEPT WITH THE CONSENT OF COUNCIL'S TOWN PLANNING DEPARTMENT & UNDER THE SUPERVISION OF A QUALIFIED ARBORIST.

ADVANCED CANOPY TREES 1.5M TALL AT TIME OF PLANTING — TREE PROTECTION ZONE BARRIER FENCE — EXISTING TREES TO BE REMOVED — EXISTING TREES TO REMAIN

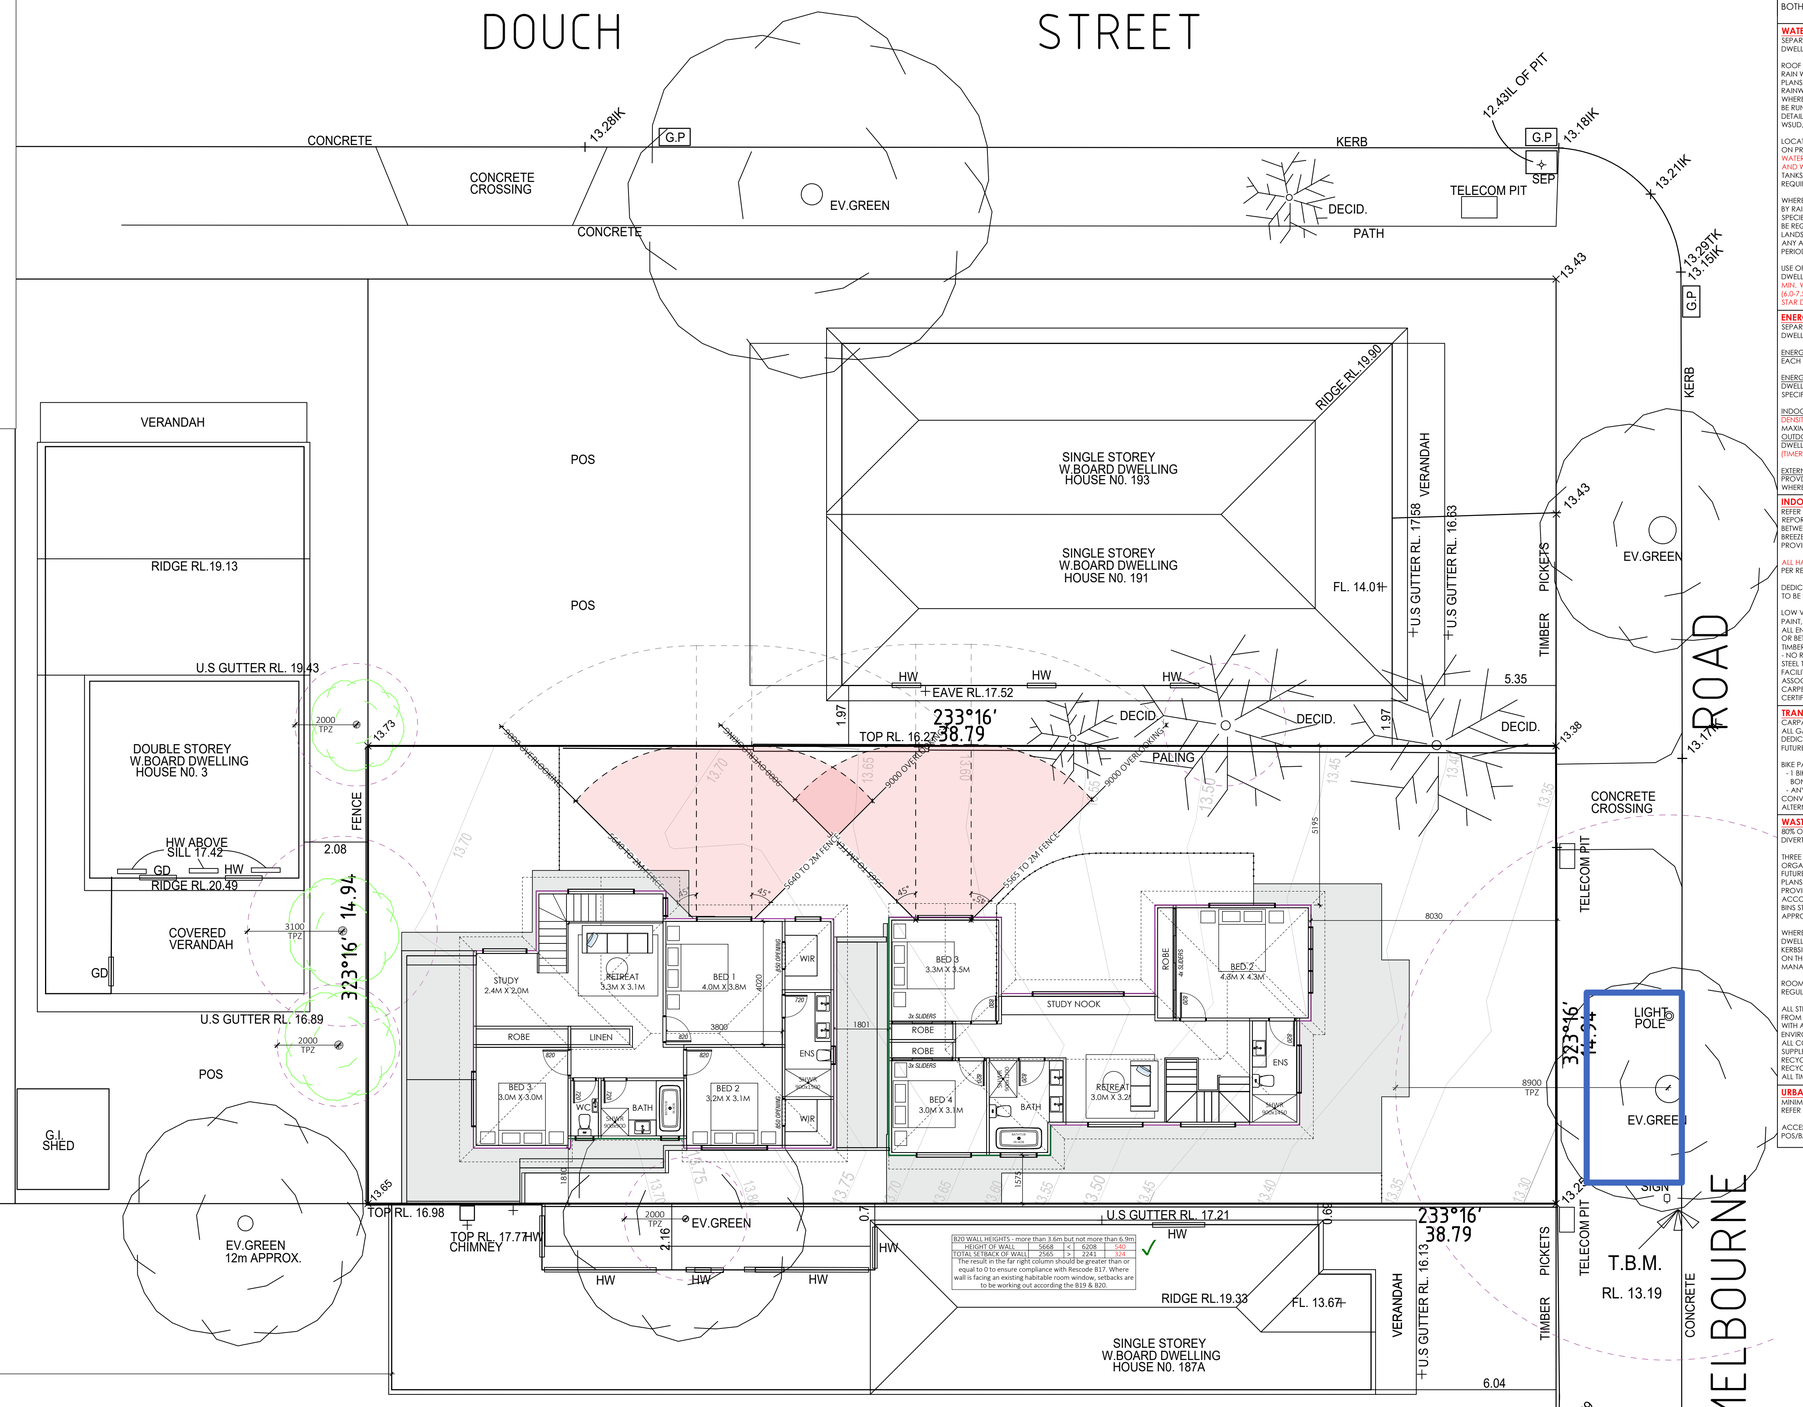

FIRST FLOOR PLAN
1:100

LENGTHS ARE IN METRES.
"LEVELS ARE TO AUSTRALIAN HEIGHT DATUM"
"PLEASE REFER TO SEPARATE PLAN FOR TITLE RE-ESTABLISHMENT SURVEY"

SDA NOTES

REFER TO SUSTAINABLE DESIGN ASSESSMENT PROVIDED BY MELBOURNE SUSTAINABILITY CONSULTANTS FOR FURTHER DETAILS.

DEVELOPMENT MUST BE CONSTRUCTED IN ACCORDANCE WITH ALL INITIATIVES INCLUDED IN BOTH SDA AND BESS REPORTS.

WATER & STORMWATER MANAGEMENT
SEPARATE UTILITY METERS TO BE PROVIDED FOR EACH DWELLING.

ROOF CATCHMENT AREA TO BE DIVERTED TO INDIVIDUAL RAIN WATER TANKS FOR EACH DWELLING - REFER WSUD PLANS. FILTERING SYSTEM TO BE USED FOR EITHER GUTTERS OR RAINWATER TANK.
WHERE REQUIRED, USE OF A CHARGED PIPE SYSTEM WILL NOT BE RUNNING UNDERNEATH THE BUILDING FOOTPRINT. DETAILS FOR ALL OTHER WATER TREATMENTS AS PER SDA, WSUD, AND LANDSCAPING PLANS.

LOCATION AND SIZE OF EACH RAINWATER TANK AS SHOWN ON PROPOSED SITE/GROUND FLOOR PLAN.
WATER TANKS TO SUPPLY WATER FOR USE IN TOILET FLUSHING AND WASHING MACHINES.
TANKS TO BE COMPLETELY SEPARATE FROM DETENTION REQUIREMENTS AS PER LEGAL POINT OF DISCHARGE.

WHERE GARDEN IRRIGATION IS REQUIRED IT WILL BE SUPPLIED BY RAINWATER TANKS. NATIVE AND/OR DROUGHT TOLERANT SPECIES WILL BE USED IN LANDSCAPING. WATERING WILL NOT BE REQUIRED AFTER INITIAL PERIOD OF ESTABLISHMENT. REFER LANDSCAPING PLAN FOR PLANT TYPES, LOCATIONS, AND ANY AREAS REQUIRING CONTINUED IRRIGATION AFTER THIS PERIOD.

USE OF WATER EFFICIENT FIXTURES AND APPLIANCES TO ALL DWELLINGS.
MIN. WELS RATINGS: 4 STAR TOILETS / 5 STAR TAPS / 4 STAR (6.0-7.5L/min) SHOWERHEAD / 5 STAR WASHING MACHINE / 5 STAR DISHWASHER.

ENERGY EFFICIENCY
SEPARATE UTILITY METERS TO BE PROVIDED FOR EACH DWELLING.

ENERGY RATING TO REACH A MINIMUM OF 7.0 STAR FOR EACH DWELLING. PRELIM INCLUDED IN SDA.

ENERGY EFFICIENT FIXTURES AND APPLIANCES TO USED IN ALL DWELLINGS. STAR RATINGS TO BE A MINIMUM OF RATING SPECIFIED IN BESS REPORT.

INDOOR LIGHTING - MAXIMUM ILLUMINATION POWER DENSITY TO BE KEPT TO 4W/SQM FOR EACH DWELLING WITH A MAXIMUM OF 3W/SQM FOR ALL GARAGES.
OUTDOOR LIGHTING - OUTDOOR LIGHTING FOR EACH DWELLING TO BE CONTROLLED BY LIGHTING SENSORS (TIMERS, MOTION SENSOR/S, ETC).

EXTERNAL CLOTHES LINE - OUTDOOR CLOTHES LINE TO BE PROVIDED FOR EACH DWELLING AS SHOWN ON PLANS, WHERE NOTATED CLOTHESLINE TO BE RETRACTABLE.

INDOOR ENVIRONMENTAL QUALITY
REFER DEVELOPMENT SUMMARY & AREAS STATED IN BESS REPORT. NORTH ORIENTATION ALLOWS FOR ORIENTATION BETWEEN 20°W AND 30°E OF TRUE NORTH.
BREEZE PATHS WHERE USING EXTERNAL DOORWAY/S MUST BE PROVIDED WITH A SECURITY INSECT SCREEN DOOR.

ALL HABITABLE ROOMS TO BE DOUBLE GLAZED OR BETTER AS PER RECOMMENDATION OF ENERGY RATER.

DEDICATED EXHAUST FAN FOR ALL KITCHEN RANGE-HOODS TO BE DIRECTLY DISCHARGED TO OUTSIDE.

LOW VOC PRODUCTS TO BE USED THROUGHOUT BUILD (INCL. PAINT, ADHESIVES, SEALANTS, FLOORING, ETC),
ALL ENGINEERED WOOD TO BE LOW FORMALDEHYDE WITH E0 OR BETTER CERTIFICATION.
TIMBER FRAMING (IF USED) TO BE CERTIFIED FEPC. AFS, OR FSC
- NO RAINFOREST TIMBER TO BE USED.
STEEL TO BE SOURCED FROM STEEL MAKER WITH ISO 14001 FACILITY AND A MEMBER OF THE WORLD STEEL ASSOCIATION'S (WSA) CLIMATE ACTION PROGRAM (CAP).
CARPET AND UNDERLAY WITH THIRD-PARTY SUSTAINABLE CERTIFICATION (GECA, CARPET INSTITUTE ECS, ETC).

TRANSPORT
CARPARKING PROVIDED AS PER RESCODE CLAUSE 52.06
ALL GARAGES TO BE PROVIDED WITH MINIMUM OF 1x 32A DEDICATED CIRCUIT FROM SWITCHBOARD TO PROVIDE FOR FUTURE ELECTRIC VEHICLE CHARGER.

BIKE PARKING ALLOWANCE: 32A VEHICLE CHARGER
- 1 BIKE SPACE PER DWELLING (NOT MOUNTED OVER BONNET). REFER FLOOR PLAN FOR LOCATIONS.
- ANY VISITOR BIKE SPACE PROVISION/S AS PER SITE PLAN.
CONVENIENCE OF BIKE PARKING IS TO PROMOTE USE OF ALTERNATIVE TRANSPORT METHODS.

WASTE
80% OF ALL CONSTRUCTION AND DEMOLITION WASTE TO BE DIVERTED FROM LANDFILL. REFER SDA.

THREE BIN SYSTEM INCLUDING RUBBISH, RECYCLING, ORGANIC/GARDEN WASTE. PROVISION OF SPACE FOR FUTURE GLASS BIN. BIN STORAGE LOCATIONS AS SHOWN ON PLANS. BIN STORAGE WITHIN ENCLOSED GARAGES TO BE PROVIDED WITH EXHAUST FANS TO BE VENTED EXTERNALLY IN ACCORDANCE WITH AS1668.2-1991
BINS STORED TO FRONT OF PROPOSAL TO BE PROVIDED WITH APPROPRIATE SCREENING.

WHERE KERB LOCATION IS RESTRICTED OR MORE THAN 5 DWELLINGS ARE PROPOSED ON THE SITE, APPROXIMATE KERBSIDE LOCATIONS FOR COLLECTION ARE TO BE SHOWN ON THE GROUND FLOOR/SITE PLAN OR A WASTE MANAGEMENT PLAN IS TO BE PROVIDED.

ROOM FOR SEPARATE RECYCLING FACILITIES WHERE REGULAR RUBBISH BINS ARE PROVIDED FOR IN ALL KITCHENS.

ALL STEEL USED IN THE DEVELOPMENT WILL BE SOURCED FROM A RESPONSIBLE STEEL MAKER I.E., MUST HAVE FACILITIES WITH A CURRENTLY VALID AND CERTIFIED ISO 14001 ENVIRONMENTAL MANAGEMENT SYSTEM (EMS).
ALL CONCRETE USED IN THE DEVELOPMENT WILL INCLUDE SUPPLEMENTARY CEMENTITIOUS MATERIAL (SCM) AND RECYCLED AGGREGATE WHERE APPROPRIATE AND RECYCLED WATER IN ITS MANUFACTURE.
ALL TIMBER USED ON SITE TO BE PEFC OR FSC CERTIFIED.

URBAN ECOLOGY
MINIMUM 10% OF SITE TO BE VEGETATED.WHERE SUPPLIED, REFER VEGETATION AREA PLAN.

ACCESS TO TAP AND FLOOR WASTE IN EACH POS/BALCONY/TERRACE (NOT SHOWN ON PLANS).

THIS PAGE IS TO BE READ IN CONJUNCTION WITH COMPLETE ARCHITECTURAL PLANS AND ALL ENGINEERING AND SHOP DRAWINGS. WORK SHALL CONFORM TO THE SPECIFICATION, SPECIALISTS REPORTS, RELEVANT AUSTRALIAN REQUIREMENTS, AND LOCAL AUTHORITY REQUIREMENTS.
FIGURED DIMENSIONS TAKE PRECEDENCE OVER SCALED WORK. BUILDER / CONTRACTOR TO VERIFY ALL DIMENSIONS & CHECK FOR DISCREPANCIES BETWEEN ARCHITECTURAL AND ALL OTHER DRAWINGS BEFORE ANY JOB COMMENCES.
THIS DRAWING IS PROTECTED BY COPY-RIGHT.
(CAD) A1

REV.	BY.	DATE.	DESCRIPTION.	REV.	BY.	DATE.	DESCRIPTION.
TP01	K.N.	02/08/24	TP SUBMISSION				
TP02	K.N.	08/10/24	RFI RESUBMISSION				
TP03	K.N.	19/11/24	RFI RESUBMISSION #1				
TP04	K.N.	01/04/25	RFI RESUBMISSION #2				

PROJECT.
TWO DOUBLE STOREY DEVELOPMENT
NO. 189 MELBOURNE ROAD
WILLIAMSTOWN ,VIC 3016

CLIENT.
--

JOB NO: MQ_24_034
DRAWN BY. MERAQ BUILDING DESIGNERS
SCALE: AS NOTATED
DATE. 11/06/2025

MERAQ building designers
MERAQ PROJECTS
29 CABOT DRIVE, ALTONA NORTH 3025
P. 03 9391 0023 ABN. 85146959775
E. admin@meraq.com.au
Dajvis Andonov DP-AD37977
Onur Ozduzenciler DP-AD33253

#
02

Received by Hobsons Bay City Council on 12/09/2025

Endorsed by Hobsons Bay City Council on 23/09/2025 under planning permit PA241413 on behalf of Hobsons Bay City Council. Sheet 4 of 7

LEGEND

- TRUSS ROOF PITCHED AS SHOWN
  COLORBOND SHEET ROOF - SOLAR ABSORBENCY ≤0.6
- BRICK, POLYSTYRENE 75MM, OR CEMENT SHEET
  LIGHT RENDER/PAINT FINISH
- BRICK, POLYSTYRENE 75MM, OR CEMENT SHEET
  DARK RENDER/PAINT FINISH
- SCYON™ LINEA™ WEATHERBOARD
  150MM/180MM PROFILE - MATCH TO RENDER
- WINDOWS - SEE SCHEDULE
  DOORS - SEE SCHEDULE
  GLAZING TRANSPARENT
- OBS. OBSCURED TRANSLUCENT GLASS

+00.54 NATURAL GROUND LEVELS TO A.H.D. UNLESS SPECIFIED OTHERWISE. FFL DENOTES FINISHED FLOOR LEVEL.

SOLAR HOT WATER SYSTEM (GAS BOOSTED) — SOLAR HOT WATER

SOLAR HOT WATER SYSTEM (GAS BOOSTED)

SIDE ON - & - FACING (22.5° ROOF)

AIR-CON EVAPORATIVE UNIT

AIR-CON SPLIT SYSTEM — HEATING & COOLING SPLIT SYSTEM EXTERNAL CONDENSER

STANDARD 2.0KW SOLAR PANEL 38° PITCH — STANDARD PHOTOVOLTAIC SOLAR PANEL AT 38° PITCH

MIN. 500MM CLEARANCE — MB — METER BOXES AND METERS
- SEE BELOW NOTES WHERE METER BOX INCLUDED IN LETTERBOX
- MINIMUM 500MM CLEARANCE BETWEEN GAS & ELECTRICAL METERS
- WHERE WALL MOUNTED KEEP A MINIMUM 600MM CLEARANCE TO ALL WINDOWS


HWS — HOT WATER SYSTEM OR BOOSTER (WHERE EXTERNAL)

NOTES


TOWN PLANNING DRAWINGS ARE TO BE READ AS A WHOLE. NOTES ONLY INCLUDED ON AN INDIVIDUAL PAGE ARE STILL REQUIRED BY THE WHOLE PROPOSAL.

WEATHERBOARD
NON-TIMBER WEATHERBOARD TO BE CONSISTENT WITH TIMBER WEATHERBOARD CLADDING PROFILES.

MAIL & METER BOX STRUCTURES
MAIL BOXES MUST BE LOCATED AT THE JUNCTION OF THE ROAD RESERVE WITH THE COMMON DRIVEWAY, FACE THE STREET TO ALLOW MAIL DELIVERY FROM THE FOOTPATH AREA AND DISPLAY THE STREET NUMBER IN ACCORDANCE WITH THE REQUIREMENTS OF AUSTRALIA POST. STRUCTURES WITH THE FRONT SETBACK MUST BE A MAXIMUM HEIGHT OF 1.2 METRES AND DESIGNED TO MINIMISE THE VISUAL IMPACT ON THE STREETSCAPE AND POSSIBLE IMPACTS ON PEDESTRIAN SAFETY AND VEHICLE TRAFFIC.
EXAMPLE SINGLE MAILBOX (NO METER BOX)

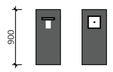

EXAMPLE MULTIPLE MAILBOX INCLUDING METERS 1:50

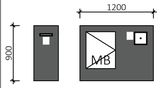

WHERE WITHIN A VISIBILITY SPLAY AS PER SITE AND GROUND FLOOR PLAN, MAIL BOX STRUCTURES TO BE A MAXIMUM OF 900MM HIGH TO ENSURE CLEAR VIEWS.

GLAZING
ALL WINDOWS AND GLAZED DOORS TO BE DOUBLE GLAZING OR BETTER AS PER ENERGY RATER RECOMMENDATION AND FINALISED ENERGY RATING REPORT.

OBSCURING
WHERE REQUIRED OBSCURED WINDOWS ARE TO BE MAXIMUM OF 25% TRANSPARENCY UP TO 1.7M FROM FFL PROVIDED BY TRANSLUCENT GLASS OR ACHIEVED WITH FIXED SCREENS WHERE SHOWN.

WALL ON BOUNDARY
MAXIMUM WALL HEIGHT ON BOUNDARY TO BE 3.2M.
ALL BRICKWORK ON OR FACING THE BOUNDARIES OF THE SITE MUST BE EITHER RAKED AND CLEANED (FACE BRICKWORK) OR RENDERED AND PAINTED OR BAGGED AND PAINTED TO THE SATISFACTION OF THE RESPONSIBLE AUTHORITY.

SERVICE PIPES, FITTINGS, & FIXTURES
EXCLUDING DOWNPIPES TO BE CONCEALED ON EXPOSED ELEVATIONS TO THE SATISFACTION OF THE RESPONSIBLE AUTHORITY. DOWNPIPES TO BE PAINTED TO MATCH WALL FINISHES WHERE NECESSARY - REFER COLOUR SCHEDULE.


SUSTAINABILITY DESIGN ASSESSMENT
WHERE ANY ADDITIONAL INFORMATION IS SUPPLIED WITHIN SDA, WSUD PLANS, STORM/MUSIC REPORTS, AND BESS REPORTS, ALL CONSTRUCTION MUST ALSO COMPLY WITH SPECIFICATIONS WITHIN THESE DOCUMENTS.

RETAINING WALLS ANY ALTERATION OF SOIL LEVEL INVOLVING AN INCREASED OR DECREASED LEVEL AT THE BOUNDARY MUST BE RETAINED BY THE PROVISION OF AN ADEQUATE RETAINING WALL, WHICH IS CONSTRUCTED OF BRICK OR MASONRY OR OTHER SUITABLE ALTERNATIVE APPROVED BY THE RESPONSIBLE AUTHORITY, TO BUTTRESS THE SOIL AGAINST THE POSSIBILITY OF SHIFT. THE CONSTRUCTION OF THIS RETAINING WALL MUST BE CARRIED OUT BY THE OWNER, THE RETAINING WALL MUST REMAIN IN PLACE WHILST ANY INCREASE OR DECREASE LEVEL IS PRESENT.
RETAINING WALL RLS BASED OFF SURVEY SPOT LEVELS& CONTOURS. FINISHED RLS AT DISCRETION OF LANDSCAPER DEPENDANT ON SITE CONDITIONS AND FINISHED GROUND LEVEL. FINISHED RLS MUST CONFORM TO MAXIMUM RETAINING WALL HEIGHTS SPECIFIED.
ALL RETAINING WALLS TO INCLUDE STANDARD DRAINAGE VIA AG1 PIPE BEHIND WALL AS PER LANDSCAPER/BUILDER.
REFER RETAINING WALL DETAILS ON L01.




NORTH EAST ELEVATION
SCALE 1:100

0.9M HIGH TIMBER PICKET FENCE PAINTED DULUX - COLOUR: VIVID WHITE

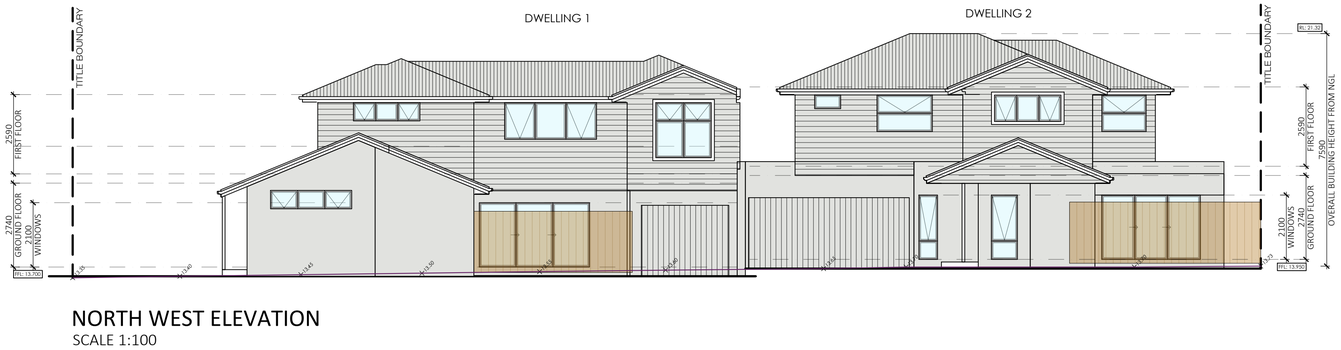


NORTH WEST ELEVATION
SCALE 1:100

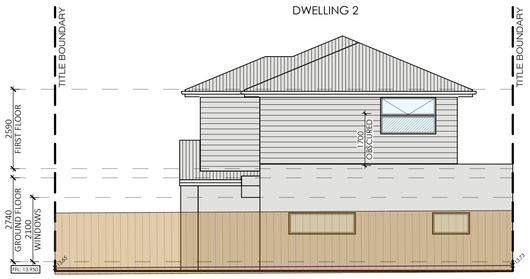

SOUTH WEST ELEVATION
SCALE 1:100



SOUTH EAST ELEVATION
SCALE 1:100

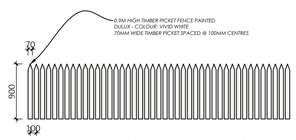


FRONT FENCE ELEVATION
SCALE 1:50




EXISTING STREET SCAPE 1:200



PROPOSED **STREET SCAPE** 1:200

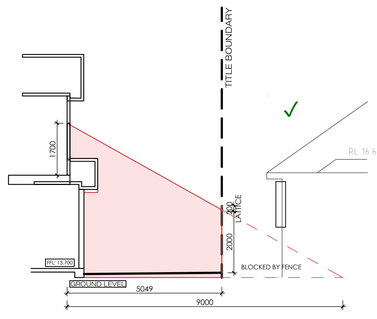

DWELLING 1 - BEDROOM 2 OVERLOOKING DIAGRAM
SCALE 1:100

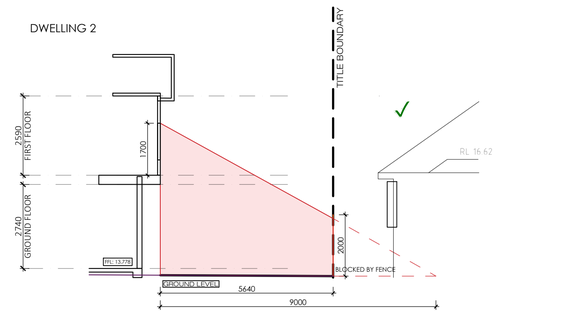

DWELLING 2 - BEDROOM 1 OVERLOOKING DIAGRAM
SCALE 1:100

ELEVATIONS
1:100

SDA NOTES

REFER TO SUSTAINABLE DESIGN ASSESSMENT PROVIDED BY MELBOURNE SUSTAINABILITY CONSULTANTS FOR FURTHER DETAILS.

DEVELOPMENT MUST BE CONSTRUCTED IN ACCORDANCE WITH ALL INITIATIVES INCLUDED IN BOTH SDA AND BESS REPORTS.

WATER & STORMWATER MANAGEMENT
SEPARATE UTILITY METERS TO BE PROVIDED FOR EACH DWELLING.

ROOF CATCHMENT AREA TO BE DIVERTED TO INDIVIDUAL RAIN WATER TANKS FOR EACH DWELLING - REFER WSUD PLANS. FILTERING SYSTEM TO BE USED FOR EITHER GUTTERS OR RAINWATER TANK.
WHERE REQUIRED, USE OF A CHARGED PIPE SYSTEM WILL NOT BE RUNNING UNDERNEATH THE BUILDING FOOTPRINT. DETAILS FOR ALL OTHER WATER TREATMENTS AS PER SDA, WSUD, AND LANDSCAPING PLANS.

LOCATION AND SIZE OF EACH RAINWATER TANK AS SHOWN ON PROPOSED SITE/GROUND FLOOR PLAN.
WATER TANKS TO SUPPLY WATER FOR USE IN TOILET FLUSHING AND WASHING MACHINES.
TANKS TO BE COMPLETELY SEPARATE FROM DETENTION REQUIREMENTS AS PER LEGAL POINT OF DISCHARGE.

WHERE GARDEN IRRIGATION IS REQUIRED IT WILL BE SUPPLIED BY RAINWATER TANKS. NATIVE AND/OR DROUGHT TOLERANT SPECIES WILL BE USED IN LANDSCAPING. WATERING WILL NOT BE REQUIRED AFTER INITIAL PERIOD OF ESTABLISHMENT. REFER LANDSCAPING PLAN FOR PLANT TYPES, LOCATIONS, AND ANY AREAS REQUIRING CONTINUED IRRIGATION AFTER THIS PERIOD.

USE OF WATER EFFICIENT FIXTURES AND APPLIANCES TO ALL DWELLINGS.
MIN. WELS RATINGS: 4 STAR TOILETS / 5 STAR TAPS / 4 STAR (6.0-7.5L/min) SHOWERHEAD / 5 STAR WASHING MACHINE / 5 STAR DISHWASHER.

ENERGY EFFICIENCY
SEPARATE UTILITY METERS TO BE PROVIDED FOR EACH DWELLING.

ENERGY RATING TO REACH A MINIMUM OF 7.0 STAR FOR EACH DWELLING. PRELIM INCLUDED IN SDA.

ENERGY EFFICIENT FIXTURES AND APPLIANCES TO USED IN ALL DWELLINGS. STAR RATINGS TO BE A MINIMUM OF RATING SPECIFIED IN BESS REPORT.

INDOOR LIGHTING - MAXIMUM ILLUMINATION POWER DENSITY TO BE KEPT TO 4W/SQM FOR EACH DWELLING WITH A MAXIMUM OF 3W/SQM FOR ALL GARAGES.
OUTDOOR LIGHTING - OUTDOOR LIGHTING FOR EACH DWELLING TO BE CONTROLLED BY LIGHTING SENSORS (TIMERS, MOTION SENSOR/S, ETC.).

EXTERNAL CLOTHES LINE - OUTDOOR CLOTHES LINE TO BE PROVIDED FOR EACH DWELLING AS SHOWN ON PLANS, WHERE NOTATED CLOTHESLINE TO BE RETRACTABLE.

INDOOR ENVIRONMENTAL QUALITY
REFER DEVELOPMENT SUMMARY & AREAS STATED IN BESS REPORT. NORTH ORIENTATION ALLOWS FOR ORIENTATION BETWEEN 20°W AND 30°E OF TRUE NORTH.
BREEZE PATHS WHERE USING EXTERNAL DOORWAYS MUST BE PROVIDED WITH A SECURITY INSECT SCREEN DOOR.

ALL HABITABLE ROOMS TO BE DOUBLE GLAZED OR BETTER AS PER RECOMMENDATION OF ENERGY RATER.

DEDICATED EXHAUST FAN FOR ALL KITCHEN RANGE-HOODS TO BE DIRECTLY DISCHARGED TO OUTSIDE.

LOW VOC PRODUCTS TO BE USED THROUGHOUT BUILD (INCL. PAINT, ADHESIVES, SEALANTS, FLOORING, ETC).
ALL ENGINEERED WOOD TO BE LOW FORMALDEHYDE WITH E0 OR BETTER CERTIFICATION.
TIMBER FRAMING (IF USED) TO BE CERTIFIED PEFC, AFS, OR FSC - NO RAINFOREST TIMBER TO BE USED.
STEEL TO BE SOURCED FROM STEEL MAKER WITH ISO 14001 FACILITY AND A MEMBER OF THE WORLD STEEL ASSOCIATION'S (WSA) CLIMATE ACTION PROGRAM (CAP).
CARPET AND UNDERLAY WITH THIRD-PARTY SUSTAINABLE CERTIFICATION (GECA, CARPET INSTITUTE ECS, ETC).

TRANSPORT
CARPARKING PROVIDED AS PER RESCODE CLAUSE 52.06
ALL GARAGES TO BE PROVIDED WITH MINIMUM OF 1x 32A DEDICATED CIRCUIT FROM SWITCHBOARD TO PROVIDE FOR FUTURE ELECTRIC VEHICLE CHARGER.

32A VEHICLE CHARGE

BIKE PARKING ALLOWANCE:
- 1 BIKE SPACE PER DWELLING (NOT MOUNTED OVER BONNET). REFER FLOOR PLAN FOR LOCATIONS.
- ANY VISITOR BIKE SPACE PROVISION/S AS PER SITE PLAN.

CONVENIENCE OF BIKE PARKING IS TO PROMOTE USE OF ALTERNATIVE TRANSPORT METHODS.

WASTE
80% OF ALL CONSTRUCTION AND DEMOLITION WASTE TO BE DIVERTED FROM LANDFILL. REFER SDA.

THREE BIN SYSTEM INCLUDING RUBBISH, RECYCLING, ORGANIC/GARDEN WASTE. PROVISION OF SPACE FOR FUTURE GLASS BIN. BIN STORAGE LOCATIONS AS SHOWN ON PLANS. BIN STORAGE WITHIN ENCLOSED GARAGES TO BE PROVIDED WITH EXHAUST FANS TO BE VENTED EXTERNALLY IN ACCORDANCE WITH AS1668.2-1991
BINS STORED TO FRONT OF PROPOSAL TO BE PROVIDED WITH APPROPRIATE SCREENING.

WHERE KERB LOCATION IS RESTRICTED OR MORE THAN 5 DWELLINGS ARE PROPOSED ON THE SITE, APPROXIMATE KERBSIDE LOCATIONS FOR COLLECTION ARE TO BE SHOWN ON THE GROUND FLOOR/SITE PLAN OR A WASTE MANAGEMENT PLAN IS TO BE PROVIDED.

ROOM FOR SEPARATE RECYCLING FACILITIES WHERE REGULAR RUBBISH BINS ARE PROVIDED FOR IN ALL KITCHENS.

ALL STEEL USED IN THE DEVELOPMENT WILL BE SOURCED FROM A RESPONSIBLE STEEL MAKER I.E., MUST HAVE FACILITIES WITH A CURRENTLY VALID AND CERTIFIED ISO 14001 ENVIRONMENTAL MANAGEMENT SYSTEM (EMS).
ALL CONCRETE USED IN THE DEVELOPMENT WILL INCLUDE SUPPLEMENTARY CEMENTITIOUS MATERIAL (SCM) AND RECYCLED AGGREGATE WHERE APPROPRIATE AND RECYCLED WATER IN ITS MANUFACTURE
ALL TIMBER USED ON SITE TO BE PEFC OR FSC CERTIFIED.

URBAN ECOLOGY
MINIMUM 10% OF SITE TO BE VEGETATED,WHERE SUPPLIED, REFER VEGETATION AREA PLAN.

ACCESS TO TAP AND FLOOR WASTE IN EACH POS/BALCONY/TERRACE (NOT SHOWN ON PLANS).

OVERLOOKING
RESCODE CLAUSE 55.04-6
STANDARD B22 & REGULATION 84

STANDARD B22
A habitable room window, balcony, terrace, deck or patio should be located and designed to avoid direct views into the secluded private open space of an existing dwelling within a horizontal distance of 9 metres (measured at ground level) of the window, balcony, terrace, deck or patio. Views should be measured within a 45 degree angle from the plane of the window or perimeter of the balcony, terrace, deck or patio, and from a height of 1.7 metres above floor level.
A habitable room window, balcony, terrace, deck or patio with a direct view into a habitable room window of existing dwelling within a horizontal distance of 9 metres (measured at ground level) of the window, balcony, terrace, deck or patio should be either:

Offset a minimum of 1.5 metres from the edge of one window to the edge of the other.
Have sill heights of at least 1.7 metres above floor level.
Have fixed, obscure glazing in any part of the window below 1.7 metre above floor level.
- Have permanently fixed external screens to at least 1.7 metres above floor level and be no more than 25 per cent transparent.

Obscure glazing in any part of the window below 1.7 metres above floor level may be openable provided that there are no direct views as specified in this standard.
Screens used to obscure a view should be:
- Perforated panels or trellis with a maximum of 25 per cent openings or solid translucent panels.
- Permanent, fixed and durable.
- Designed and coloured to blend in with the development.

This standard does not apply to a new habitable room window, balcony, terrace, deck or patio which faces a property boundary where there is a visual barrier at least 1.8 metres high and the floor level of the habitable room, balcony, terrace, deck or patio is less than 0.8 metres above ground level at the boundary.

THIS PAGE IS TO BE READ IN CONJUNCTION WITH COMPLETE ARCHITECTURAL PLANS AND ALL ENGINEERING AND SHOP DRAWINGS. WORK SHALL CONFORM TO THE SPECIFICATION, SPECIALISTS REPORTS, RELEVANT AUSTRALIAN REQUIREMENTS, AND LOCAL AUTHORITY REQUIREMENTS.
FIGURED DIMENSIONS TAKE PRECEDENCE OVER SCALED WORK. BUILDER / CONTRACTOR TO VERIFY ALL DIMENSIONS & CHECK FOR DISCREPANCIES BETWEEN ARCHITECTURAL AND ALL OTHER DRAWINGS BEFORE ANY JOB COMMENCES.
THIS DRAWING IS PROTECTED BY COPY-RIGHT.
(CAD) A1

REV.	BY.	DATE.	DESCRIPTION.	REV.	BY.	DATE.	DESCRIPTION.
TP01	K.N.	02/08/24	TP SUBMISSION				
TP02	K.N.	08/10/24	RFI RESUBMISSION				
TP03	K.N.	19/11/24	RFI RESUBMISSION #1				
TP04	K.N.	01/04/25	RFI RESUBMISSION #2				

PROJECT.
TWO DOUBLE STOREY DEVELOPMENT
NO. 189 MELBOURNE ROAD
WILLIAMSTOWN ,VIC 3016

CLIENT.
--

JOB NO: MQ_24_034
SCALE: AS NOTATED
DRAWN BY. MERAQ BUILDING DESIGNERS
DATE. 11/06/2025

MERAQ building designers

MERAQ PROJECTS
29 CABOT DRIVE, ALTONA NORTH 3025
P. 03 9391 0023 ABN. 85146959775
E. admin@meraq.com.au
Dajvis Andonov DP-AD37977
Onur Ozduzenciler DP-AD33253

03

Received by Hobsons Bay City Council on 12/09/2025

Endorsed by Rhiannon Wright on 23/09/2025 under planning permit PA241413 on behalf of Hobsons Bay City Council. Sheet 5 of 7

LENGTHS ARE IN METRES.

"LEVELS ARE TO AUSTRALIAN HEIGHT DATUM"

"PLEASE REFER TO SEPARATE PLAN FOR TITLE RE-ESTABLISHMENT SURVEY"

TREE MANAGEMENT PLAN
1:100

THIS PAGE IS TO BE READ IN CONJUNCTION WITH COMPLETE ARCHITECTURAL PLANS AND ALL ENGINEERING AND SHOP DRAWINGS. WORK SHALL CONFORM TO THE SPECIFICATION, SPECIALISTS REPORTS, RELEVANT AUSTRALIAN REQUIREMENTS, AND LOCAL AUTHORITY REQUIREMENTS.
FIGURED DIMENSIONS TAKE PRECEDENCE OVER SCALED WORK. BUILDER / CONTRACTOR TO VERIFY ALL DIMENSIONS & CHECK FOR DISCREPANCIES BETWEEN ARCHITECTURAL AND ALL OTHER DRAWINGS BEFORE ANY JOB COMMENCES.
THIS DRAWING IS PROTECTED BY COPY-RIGHT.
(CAD) A1

REV.	BY.	DATE.	DESCRIPTION.	REV.	BY.	DATE.	DESCRIPTION.
TP01	K.N.	02/08/24	TP SUBMISSION				
TP02	K.N.	08/10/24	RFI RESUBMISSION				
TP03	K.N.	19/11/24	RFI RESUBMISSION #1				
TP04	K.N.	01/04/25	RFI RESUBMISSION #2				

PROJECT.
TWO DOUBLE STOREY DEVELOPMENT
NO. 189 MELBOURNE ROAD
WILLIAMSTOWN ,VIC 3016

CLIENT.
--

JOB NO: MQ_24_034	DRAWN BY. MERAQ BUILDING DESIGNERS
SCALE: AS NOTATED	DATE. 11/06/2025

MERAQ
building designers

MERAQ PROJECTS
29 CABOT DRIVE, ALTONA NORTH 3025
P. 03 9391 0023 ABN. 85146959775
E. admin@meraq.com.au
Dajvis Andonov DP-AD37977
Onur Ozduzenciler DP-AD33253

#
TMP

Received by Hobsons Bay City Council on 12/09/2025

Endorsed with changes dated 23/09/2025 under planning permit PA241413 on behalf of Hobsons Bay City Council. Sheet 6 of 7

LEGEND

- COLOURED CONCRETE - AS PER COLOUR SCHEDULE SOLAR ABSORBENCY ≤0.7
- LAWN AND LANDSCAPED AREAS
- GARDEN BED - BLACK OR RED MULCH
- GROUND FLOOR ROOF UNDER (FIRST FLOOR PLAN ONLY)
- STORAGE — 6M3 STORAGE AREA PER DWELLING - HEIGHT TO BE LESS THAN ANY ADJACENT FENCING - GARAGE OVER-CAR STORAGE TO BE SHOWN IN ADDITIONAL DIAGRAM
- CLOTHESLINE — FREE-STANDING CLOTHESLINE - NOT TO BE MOUNTED ON FENCES OR BOUNDARY WALLS - HEIGHT TO BE MAX. 1.8M
- 2000L WATER TANK — WATER TANK/S -OR- SOLAR HOT WATER. EACH DWELLING TO HAVE EITHER A WATER TANK OR A SOLAR HOT WATER SYSTEM. (SOLAR HOT WATER SYSTEM (GAS BOOSTED))
- 2000L WATER TANK (UNDER DECK)
- BINS AS PER INDIVIDUAL COUNCIL REQUIREMENTS - WHERE LOCATED WITHIN GARAGES, EXHAUST FAN TO BE PROVIDED - WHERE LOCATED IN FRONT OF DWELLINGS, SCREENING AS NOTATED
- LETTER BOXES AS PER ELEVATIONS - NUMBERED AS PER DWELLING
- INDIVIDUAL CONCRETE PAVERS - SPACED TO ALLOW MIN. 20% PERMEABILITY
- METER BOXES AND METERS
- HWS — HOT WATER SYSTEM OR BOOSTER (WHERE EXTERNAL)
- H/AC — HEATING & COOLING SPLIT SYSTEM EXTERNAL CONDENSER
- SMOKE DETECTERS AS PER AS3786
- EXHAUST FANS VENTED EXTERNALLY AS PER AS1668.2
- +RL205.54 — NATURAL GROUND LEVELS TO A H.D. UNLESS SPECIFIED OTHERWISE. FFL DENOTES FINISHED FLOOR LEVEL.
- EXISTING FENCE/S

NOTES

TOWN PLANNING DRAWINGS ARE TO BE READ AS A WHOLE. NOTES ONLY INCLUDED ON AN INDIVIDUAL PAGE ARE STILL REQUIRED BY THE WHOLE PROPOSAL.

VEGETATION TO COVER AT MINIMUM 20%OF THE SITE.

ARBORIST REPORT - ALL WORKS TO BE CARRIED OUT IN ACCORDANCE WITH ARBORIST REPORT DATED 24TH OCTOBER 20204 PREPARED BY STEM ARBORICULTURE.

ALL STORM WATER INFRASTRUCTURE AS REQUIRED BY CONDITIONS OF THE PLANNING PERMIT ARE TO BE LOCATED WITHIN THE DRIVEWAY AND NOT IN THE AREAS SET ASIDE FOR LANDSCAPING.

STREET TREE/S
REFER NOTES ON PLAN FOR WHETHER STREET TREES REQUIRE PROTECTION, REMOVAL, REPLACEMENT, OR ARE TO BE PLANTED. TREE PROTECTION ZONES AS PER NOTES BELOW. ALL CHANGES TO STREETSCAPE LANDSCAPING ARE TO BE DONE BY THE RESPONSIBLE AUTHORITY AT THE COST OF OWNER.

SITE CLEARING
IT IS THE RESPONSIBILITY OF THE OWNER TO UNDERTAKE TREE REMOVAL INCLUDING OBTAINING ANY ASSOCIATED PERMITS, AND TO PROVIDE A SITE CLEAR OF ANY VEGETATION & DEBRIS TO THE SATISFACTION OF THE BUILDER PEIOR TO THE COMMENCEMENT OF SITEWORKS.REFER TO PLANS FOR ALL EXISTING TREES TO BE RETAINED.IT IS THE RESPONSIBILITY OF THE OWNER TO UNDERTAKE REMOVAL OF ANY SITE SOIL/STOCK PILES TO THE SATISFACTION OF THE BUILDER PRIOR TO COMMENCEMENT OF CONSTRUCTION OR A COST VARIATION WILL NE INCURRED.

IRRIGATION
WHERE LANDSCAPED AREAS WILL REQUIRE WATERING AFTER THE INITIAL ESTABLISHMENT PERIOD, THOSE AREAS ON THE SITE TO BE SERVICED BY A FULLY AUTOMATED IRRIGATION SYSTEM OR MANUALLY OPERATED SYSTEM WITH TIMER(S) TO THE SATISFACTION OF THE RESPONSIBLE AUTHORITY.
PROVIDE CONDUITS UNDER HARD SERVICES TO ENABLE CABLING & PLUMBING BETWEEN LANDSCAPED AREAS. INSTALL SEPARATE IRRIGATION LINES FOR LAWNS & GARDEN BEDS WITH DRIPPER SYSTEM PROVISION TO ALL GARDENS.
ALL MANUAL AND DRIP IRRIGATION SYSTEMS TO CONNECT TO RAINWATER TANK WHERE POSSIBLE.

MAINTENANCE
LANDSCAPE TO BE KEPT IN A NEAT & TIDY CONDITION AT ALL TIMES BY REGULAR ROUTINE MAINTENANCE ACTIVITIES INCLUDING :
- WATERING THROUGH INITIAL PLAN ESTABLISHMENT PERIOD.
- CHECKING IRRIGATION SYSTEM
- REPLACING DEAD & DISEASED PLANTS
- WEED REMOVAL
- DEAD HEADING
- TRIMMING FOR SHAPE & DENSITY
- FORMATIVE TREE PRUNING
- TOPPING UP GRAVEL SURFACING & MULCH DEPTHS
- FERTILIZING
- RE-SEEDING / RE-TURFING & MOWING
- REMOVAL OF STAKES, TREE TIES & WATER WELLS AFTER 2YEARS

PARTY RESPONSIBLE FOR ONGOING MAINTENANCE OF LANDSCAPED AREAS: INDIVIDUAL DWELLING OCCUPANTS. BODY CORPORATE RESPONSIBLE FOR ANY AREAS LABELLED IN DEVELOPMENT SUMMARY AS SHARED OR COMMON.

TREE PROTECTION ZONES

A SUITABLE TREE PROTECTION ZONE OF 1.0M RADIUS WITH BARRIER FENCE MUST BE ESTABLISHED AROUND THE EXISTING STREET TREE ON THE SUBJECT SITE. THIS FENCE MUST NOT ENCLOSE THE FOOTPATH WHICH MUST BE KEPT CLEAR FOR PEDESTRIAN ACCESS AND A SIGN MUST BE ERECTED ON THE FENCE INFORMING THAT THE FENCE IS A 'TREE PROTECTION ZONE'.

TREE PROTECTION ZONE/S MUST BE ENCLOSED USING A 2 METER HIGH TEMPORARY CYCLONE FENCE OR SIMILAR WHICH MUST REMAIN IN PLACE THROUGH ALL STAGES OF THE DEVELOPMENT. THIS FENCE MUST NOT ENCLOSE THE FOOTPATH WHICH MUST BE KEPT CLEAR FOR PEDESTRIAN ACCESS AND A SING MUST BE ERECTED ON THE FENCE INFORMING THAT THE FENCE IS A TREE PROTECTION ZONE: THE AREA WITHIN THE TREE PROTECTION ZONE MUST NOT BE DISTURBED BY ANY MEANS (INCL. PARKING OF VEHICLES OR STORAGE OF PLANT & EQUIPMENT, MATERIALS, SOIL OR WASTE). NO EXCAVATION IS ALLOWED WITHIN THE TREE PROTECTION ZONE EXCEPT WITH THE CONSENT OF COUNCILS TOWN PLANNING DEPARTMENT & UNDER THE SUPERVISION OF A QUALIFIED ARBORSIT.


ADVANCED CANOPY TREES 1.5M TALL AT TIME OF PLANTING — TREE PROTECTION ZONE BARRIER FENCE — EXISTING TREES TO BE REMOVED — EXISTING TREES TO REMAIN

LANDSCAPING PLANT SCHEDULE

CODE	PLAN	BOTANICAL NAME	TYPE	W	INFO	AT MATURITY HEIGHT	AT MATURITY WIDTH	POT SIZE ØDIA	QTY
AI		ACACIA IMPLEXA (HICKORY WATTLE/LIGHTWOOD)	MED TREE	DR	N, EG, F	10,000mm*	6,000mm	ADVANCED	4
DG	DG	DIETES GRANDIFLORA (WILD IRIS, BUTTERFLY GRASS)	GRASSES	DR	EG, F	1,200mm	750mm	250mm DIA	7
A	A	ANIGOZANTHOS (KANGAROO PAW AMBER VELVET)	GRASSES	DR	N, EG, F	900mm	500mm	150mm DIA	7
PA	PA	PENNISETUM ALOPECUROIDES (SWAMP GRASS)	GRASSES	RG	N, EG, F	700mm	500mm	150mm DIA	55
-		KIKUYU GRASS (PENNISETUM CLANDESTINUM)	LAWN	DR	EG	3-4cm**	N/A	TURF ROLLS	LAWN

W (Water): DR = Drought Resistant, RW = REGULAR WATERING, RG = Rain Garden appropriate plants suitable for inconsistant watering (dry spells and heavy rain areas).
INFO: N = Native, D = Deciduous, EG = Evergreen, F = Flowering, E = Food Producing, SH = Shallow Root (for use in easements)
*Canopy trees (MED and LRG) to be 1.5m tall at time of planting. Tree size guide: SML < 8m ≤ MED ≤ 12m < LRG
**Lawn heights given as recommended maintenance heights when mowing. Lawn QTY to be measured by supplier to suit turf roll sizes available.
N.B. Rain Garden appropriate plants may be used in regular garden areas. Rain Gardens to be hatched as per legend. See WSUD for Rain Garden sizes and construction.



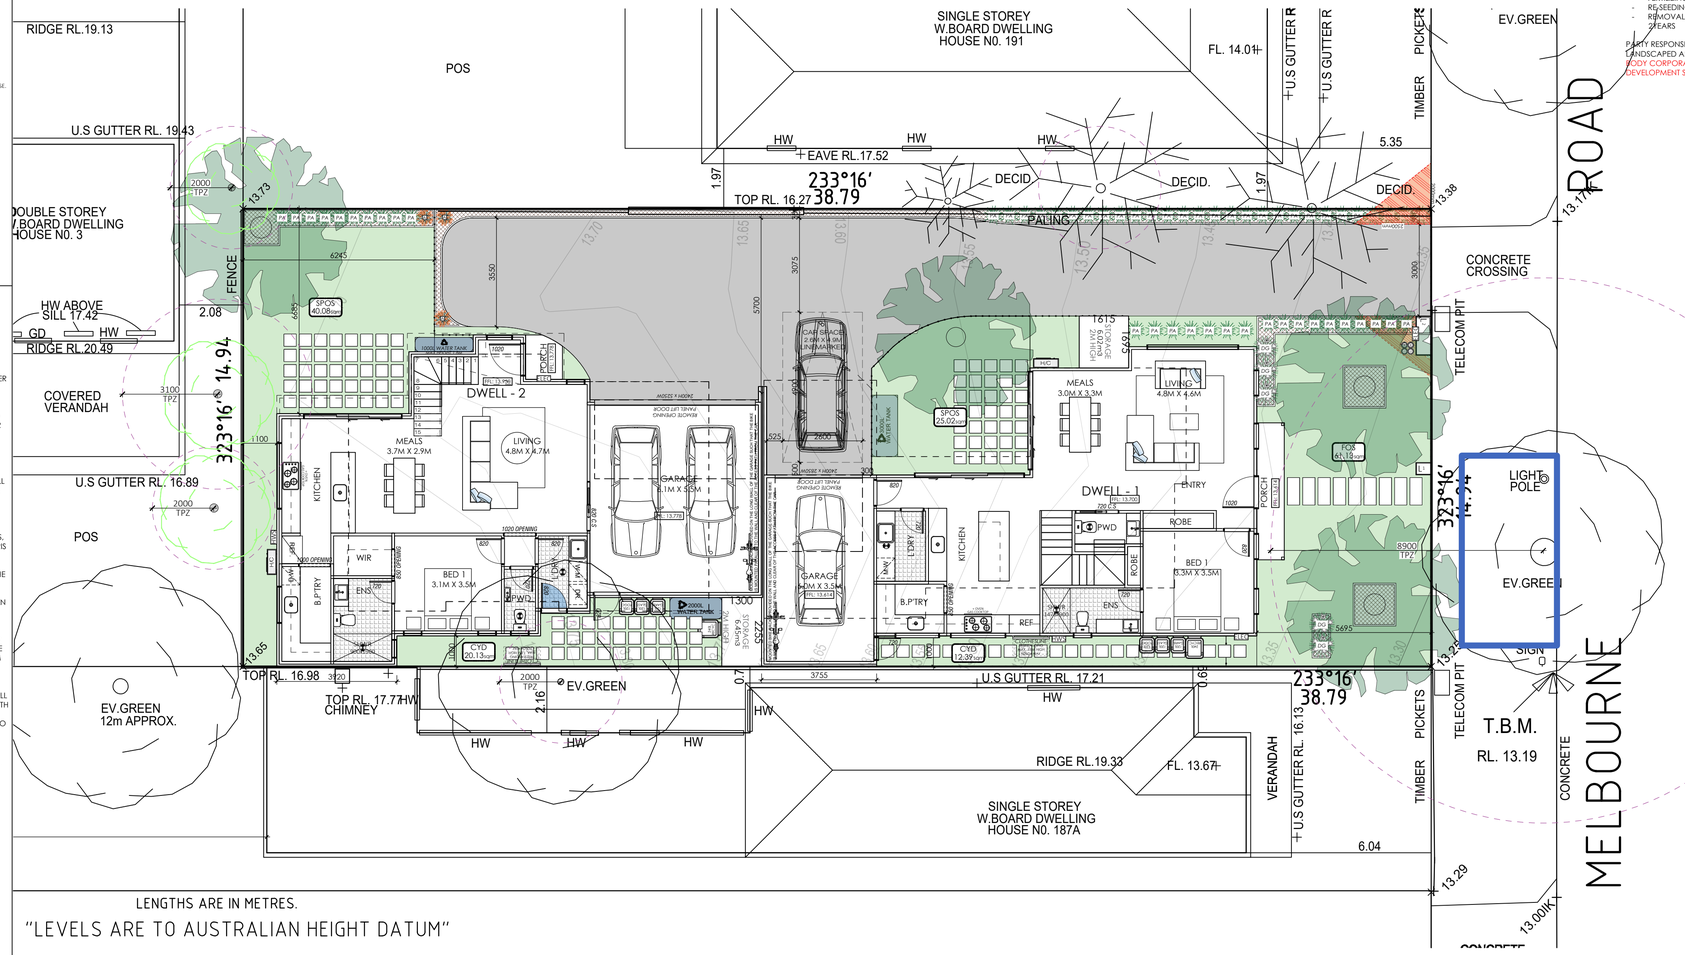

LANDSCAPE PLAN
1:100

TREES

PROPOSED TREES
CANOPY TREES TO BE 1.5M TALL AT TIME OF PLANTING.

EXISTING TREES
EXISTING TREES ON SITE THAT ARE PROPOSED TO BE KEPT ARE TO BE PROTECTED DURING ALL STAGES OF THE BUILD AND SITE WORKS AS PER ARBORIST REPORT.

STREET TREES
REFER NOTES ON PLAN FOR WHETHER STREET TREES REQUIRE PROTECTION, REMOVAL, REPLACEMENT, OR ARE TO BE PLANTED. TREE PROTECTION ZONES AS PER NOTES BELOW. ALL CHANGES TO STREETSCAPE LANDSCAPING ARE TO BE DONE BY THE RESPONSIBLE AUTHORITY AT THE COST OF OWNER.


NEIGHBOURING TREES
ARBORIST REPORT TO BE FOLLOWED FOR PROTECTION OF NEIGHBOURING TREES, WHERE NO ARBORIST REPORT REQUIRED, SUITABLE CARE IS TO BE TAKEN TO PROTECT NEIGHBOURING TREES CLOSE TO THE PROPOSED LOT.

ALL OTHER PLANTS


IRRIGATION
WHERE LANDSCAPED AREAS WILL REQUIRE WATERING AFTER THE INITIAL ESTABLISHMENT PERIOD, THOSE AREAS ON THE SITE TO BE SERVICED BY A FULLY AUTOMATED IRRIGATION SYSTEM OR MANUALLY OPERATED SYSTEM WITH TIMER(S) TO THE SATISFACTION OF THE RESPONSIBLE AUTHORITY.
PROVIDE CONDUITS UNDER HARD SERVICES TO ENABLE CABLING & PLUMBING BETWEEN LANDSCAPED AREAS. INSTALL SEPARATE IRRIGATION LINES FOR LAWNS & GARDEN BEDS WITH DRIPPER SYSTEM PROVISION TO ALL GARDENS.
ALL MANUAL AND DRIP IRRIGATION SYSTEMS TO CONNECT TO RAINWATER TANK WHERE POSSIBLE.

MAINTENANCE
LANDSCAPE TO BE KEPT IN A NEAT & TIDY CONDITION AT ALL TIMES BY REGULAR ROUTINE MAINTENANCE ACTIVITIES INCLUDING :
- WATERING THROUGH INITIAL PLAN ESTABLISHMENT PERIOD.
- CHECKING IRRIGATION SYSTEM
- REPLACING DEAD & DISEASED PLANTS
- WEED REMOVAL
- DEAD HEADING
- TRIMMING FOR SHAPE & DENSITY
- FORMATIVE TREE PRUNING
- TOPPING UP GRAVEL SURFACING & MULCH DEPTHS
- FERTILIZING
- RE-SEEDING / RE-TURFING & MOWING
- REMOVAL OF STAKES, TREE TIES & WATER WELLS AFTER 2YEARS


PARTY RESPONSIBLE FOR ONGOING MAINTENANCE OF LANDSCAPED AREAS: INDIVIDUAL DWELLING OCCUPANTS. BODY CORPORATE RESPONSIBLE FOR ANY AREAS LABELLED IN DEVELOPMENT SUMMARY AS SHARED OR COMMON.

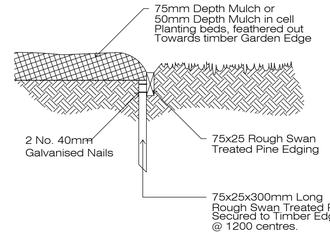

GARDEN BED TIMBER EDGE
NOT TO SCALE

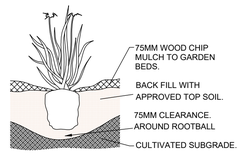


SHRUB PLANTING DETAIL
NOT TO SCALE

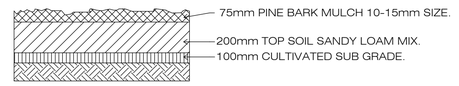


DETAIL SURFACE
NOT TO SCALE



DETAIL SURFACE
NOT TO SCALE

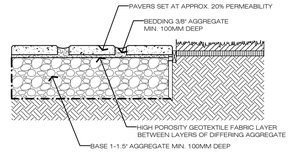

PERMEABLE PAVING DETAIL
NOT TO SCALE

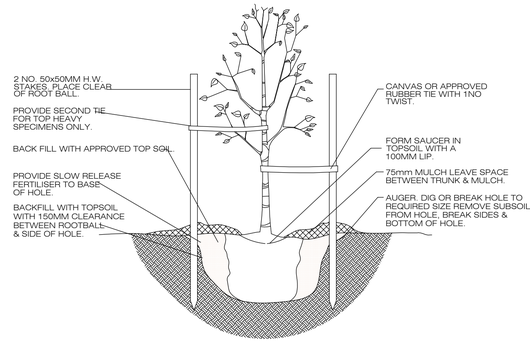

TREE PLANTING DETAIL
NOT TO SCALE

THIS PAGE IS TO BE READ IN CONJUNCTION WITH COMPLETE ARCHITECTURAL PLANS AND ALL ENGINEERING AND SHOP DRAWINGS. WORK SHALL CONFORM TO THE SPECIFICATION, SPECIALISTS REPORTS, RELEVANT AUSTRALIAN REQUIREMENTS, AND LOCAL AUTHORITY REQUIREMENTS.
FIGURED DIMENSIONS TAKE PRECEDENCE OVER SCALED WORK. BUILDER / CONTRACTOR TO VERIFY ALL DIMENSIONS & CHECK FOR DISCREPANCIES BETWEEN ARCHITECTURAL AND ALL OTHER DRAWINGS BEFORE ANY JOB COMMENCES.
THIS DRAWING IS PROTECTED BY COPY-RIGHT.
(CAD) A1

REV.	BY.	DATE.	DESCRIPTION.	REV.	BY.	DATE.	DESCRIPTION.
TP01	K.N.	02/08/24	TP SUBMISSION				
TP02	K.N.	08/10/24	RFI RESUBMISSION				
TP03	K.N.	19/11/24	RFI RESUBMISSION #1				
TP04	K.N.	01/04/25	RFI RESUBMISSION #2				

PROJECT.
TWO DOUBLE STOREY DEVELOPMENT
NO. 189 MELBOURNE ROAD
WILLIAMSTOWN ,VIC 3016

CLIENT.
--

JOB NO: MQ_24_034 | DRAWN BY. MERAQ BUILDING DESIGNERS
SCALE: AS NOTATED | DATE. 11/06/2025

MERAQ building designers
MERAQ PROJECTS
29 CABOT DRIVE, ALTONA NORTH 3025
P. 03 9391 0023 ABN. 85146959775
E. admin@meraq.com.au
Dajvis Andonov DP-AD37977
Onur Ozduzenciler DP-AD33253

L1

Received by Hobsons Bay City Council on 12/09/2025


Endorsed by Rhiannon Wright on 23/09/2025 under planning permit PA241413 on behalf of Hobsons Bay City Council. Sheet 7 of 7

MERAQ
building designers

PO BOX.310 WILLIAMSTOWN 3016 P. 03 9391 0023 E. admin@meraq.com.au

NO. 189 MELBOURNE ROAD, WILLIAMSTOWN

COLOURS & MATERIALS SCHEDULE

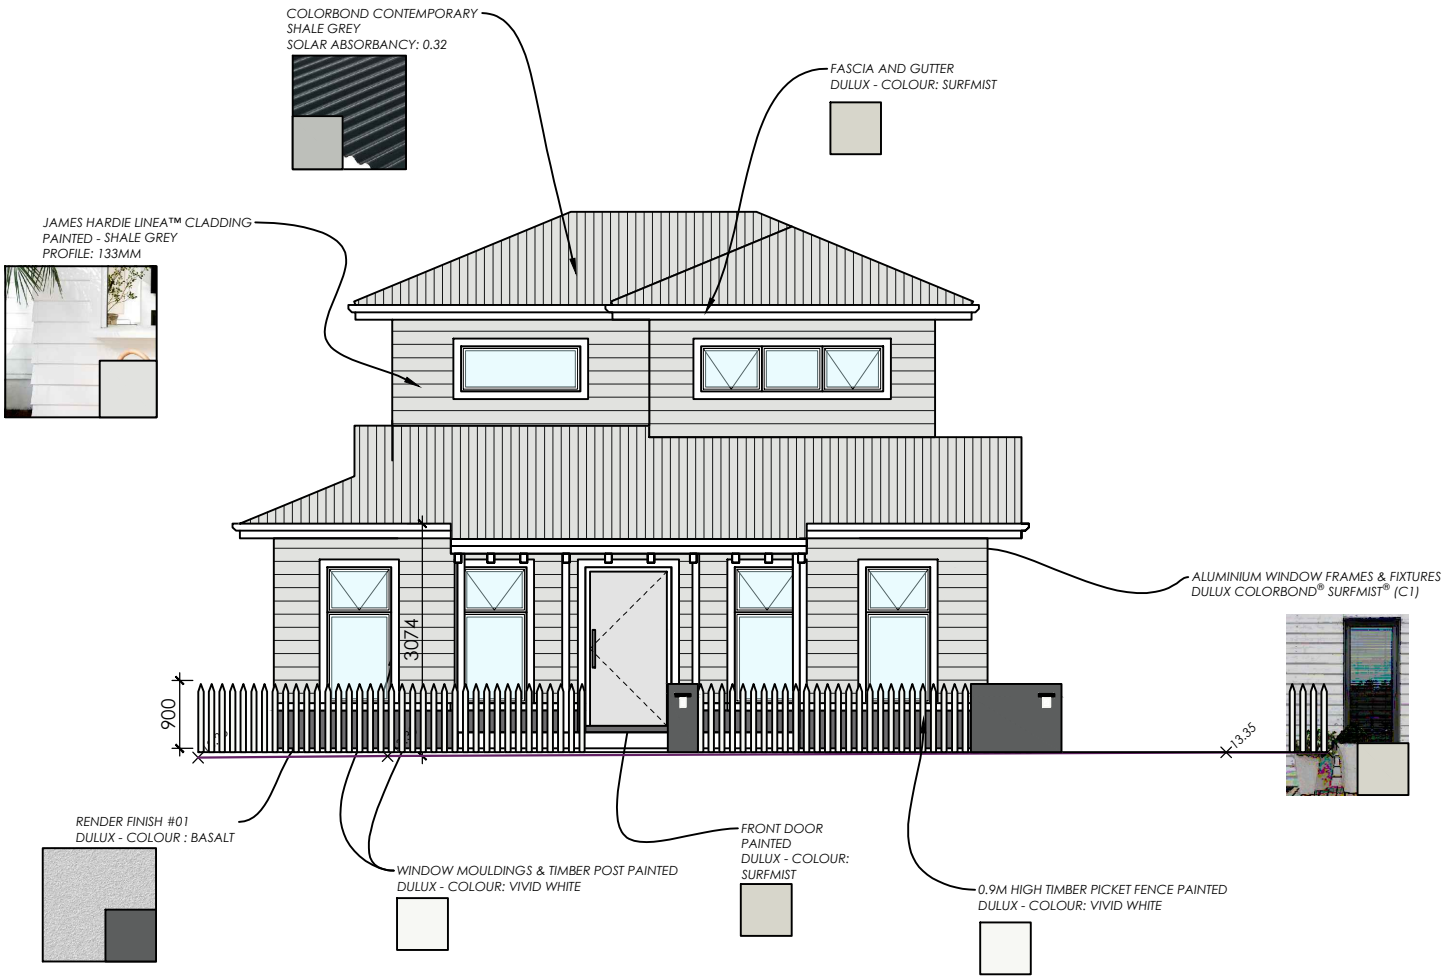

OTHER MATERIALS AND COLOURS



DRIVEWAY COLOURED
CONCRETE
BORAL CONCRETE
COLOUR - ORACLE

SOLAR ABSORBANCY: 0.47 APPROX.



JAMES HARDIE AXON™ CLADDING
PAINTED - DULUX
PROFILE: 133MM OR 400MM

INSET OF FINISH COLOUR
SURFMIST® (C1)

THE COLOURS SHOWN REPRESENT ACTUAL PRODUCT COLOURS AS ACCURATELY AS POSSIBLE HOWEVER MAY VARY SLIGHTLY IN TONE AND FINISH DUE TO BEING SHOWN VIA COMPUTER SCREEN OR PAPER, OR ALTERNATIVELY DUE TO PRINTER DIFFERENCES OR INDIVIDUAL BATCH MAKE-UP. WHERE COLOUR OF PICTURE DOES NOT MATCH SPECIFIED COLOUR, ASSUME PRINTER ERROR & REFER WRITTEN COLOUR FOR ITEM.